


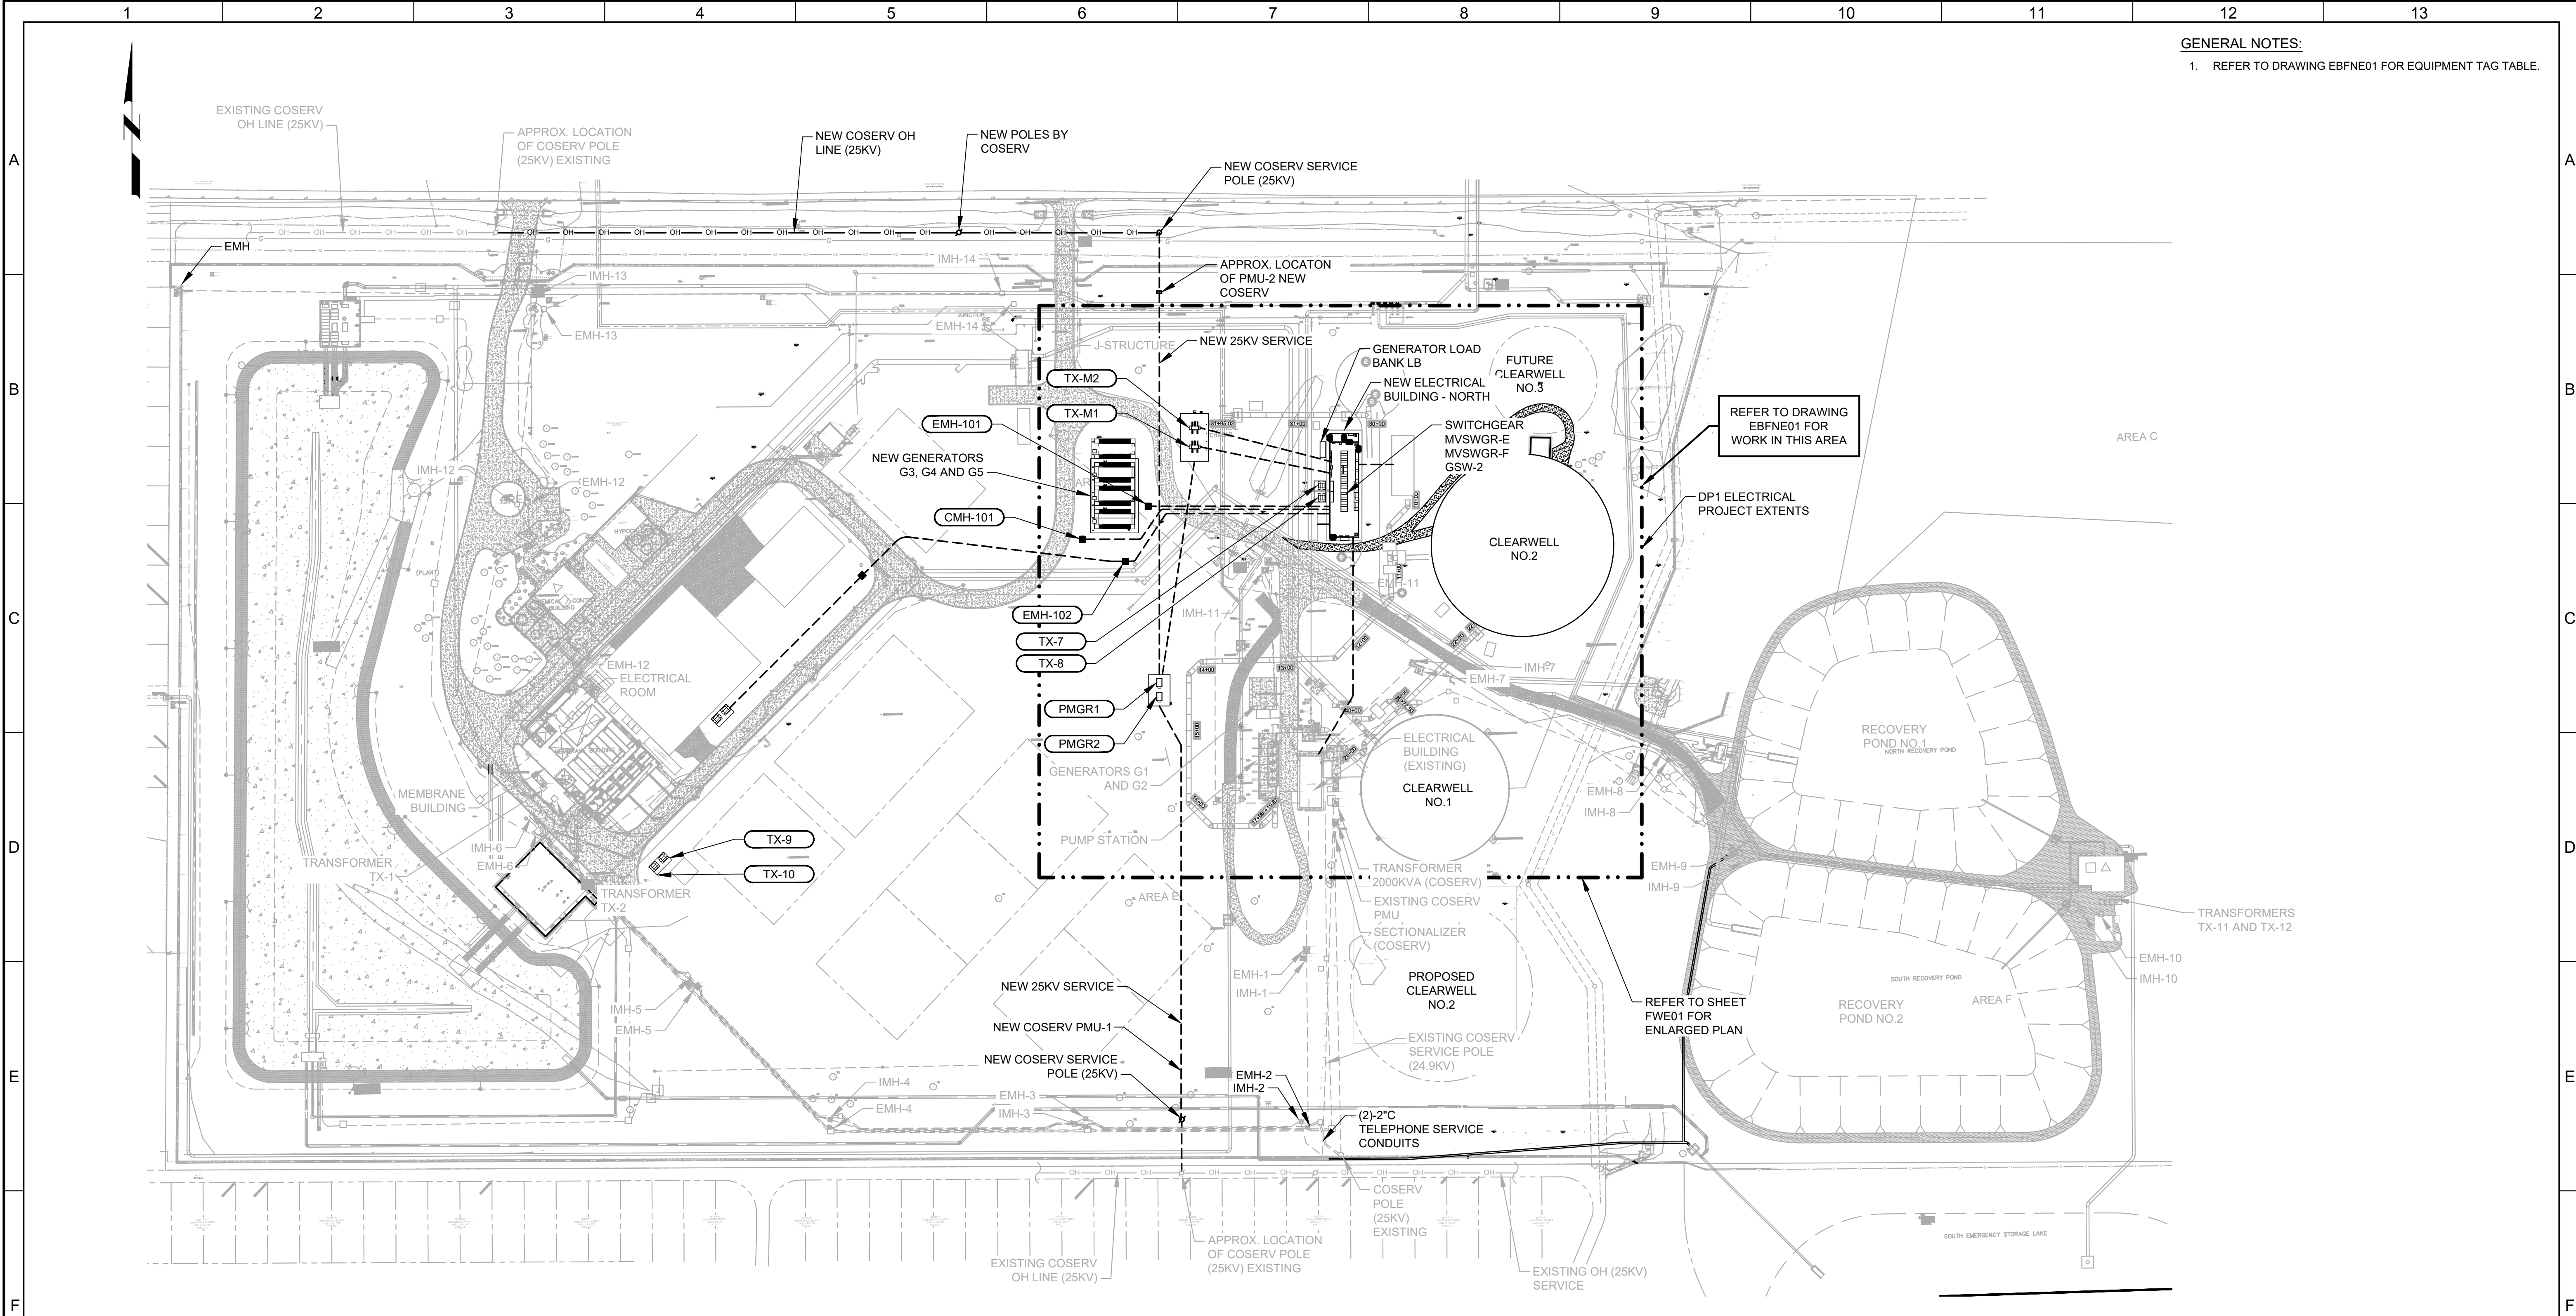

GENERAL NOTES:
1. REFER TO DRAWING EBFNE01 FOR EQUIPMENT TAG TABLE.

OVERALL SITE
A PLAN
SCALE: 1" = 100'
FILE:

THIS DRAWING IS ISSUED FOR THE
PURPOSE OF PROCUREMENT
ONLY, AND SHALL NOT BE USED
FOR CONSTRUCTION PURPOSES

GAI
Gupta & Associates, Inc.
CONSULTING ENGINEERING
Registration No. F-2593
13717 Neutron Road
Dallas, Texas 75244
Tel: 972-490-7661
Fax: 972-490-7125
email: vkgupta@gaiconsulting.com

LAST SAVED BY: M. CHAMBERLIN

INTERMEDIATE DESIGN SUBMITTAL NOT FOR CONSTRUCTION			
REV	DATE	BY	DESCRIPTION
1			
2			
3			

DESIGNED AG
DRAWN MAC
CHECKED MA
DATE OCTOBER 2024


This document is released for the purpose of information exchange review and planning only under the authority of V. K. Gupta, P.E. (Texas License No. 115692) on October 2024. It is not to be used for bidding, permit or construction purposes.


carollo
TBPELS No. F-882



UPPER TRINITY REGIONAL WATER DISTRICT
TOM HARPOOL REGIONAL WTP
PHASE 2 EXPANSION PROJECT - DESIGN PACKAGE 1
ELECTRICAL
**OVERALL SITE PLAN
MODIFIED**

VERIFY SCALES BAR IS ONE INCH ON ORIGINAL DRAWING 0 1"	JOB NO. 202056 DRAWING NO. E02 SHEET NO. X OF
--	---

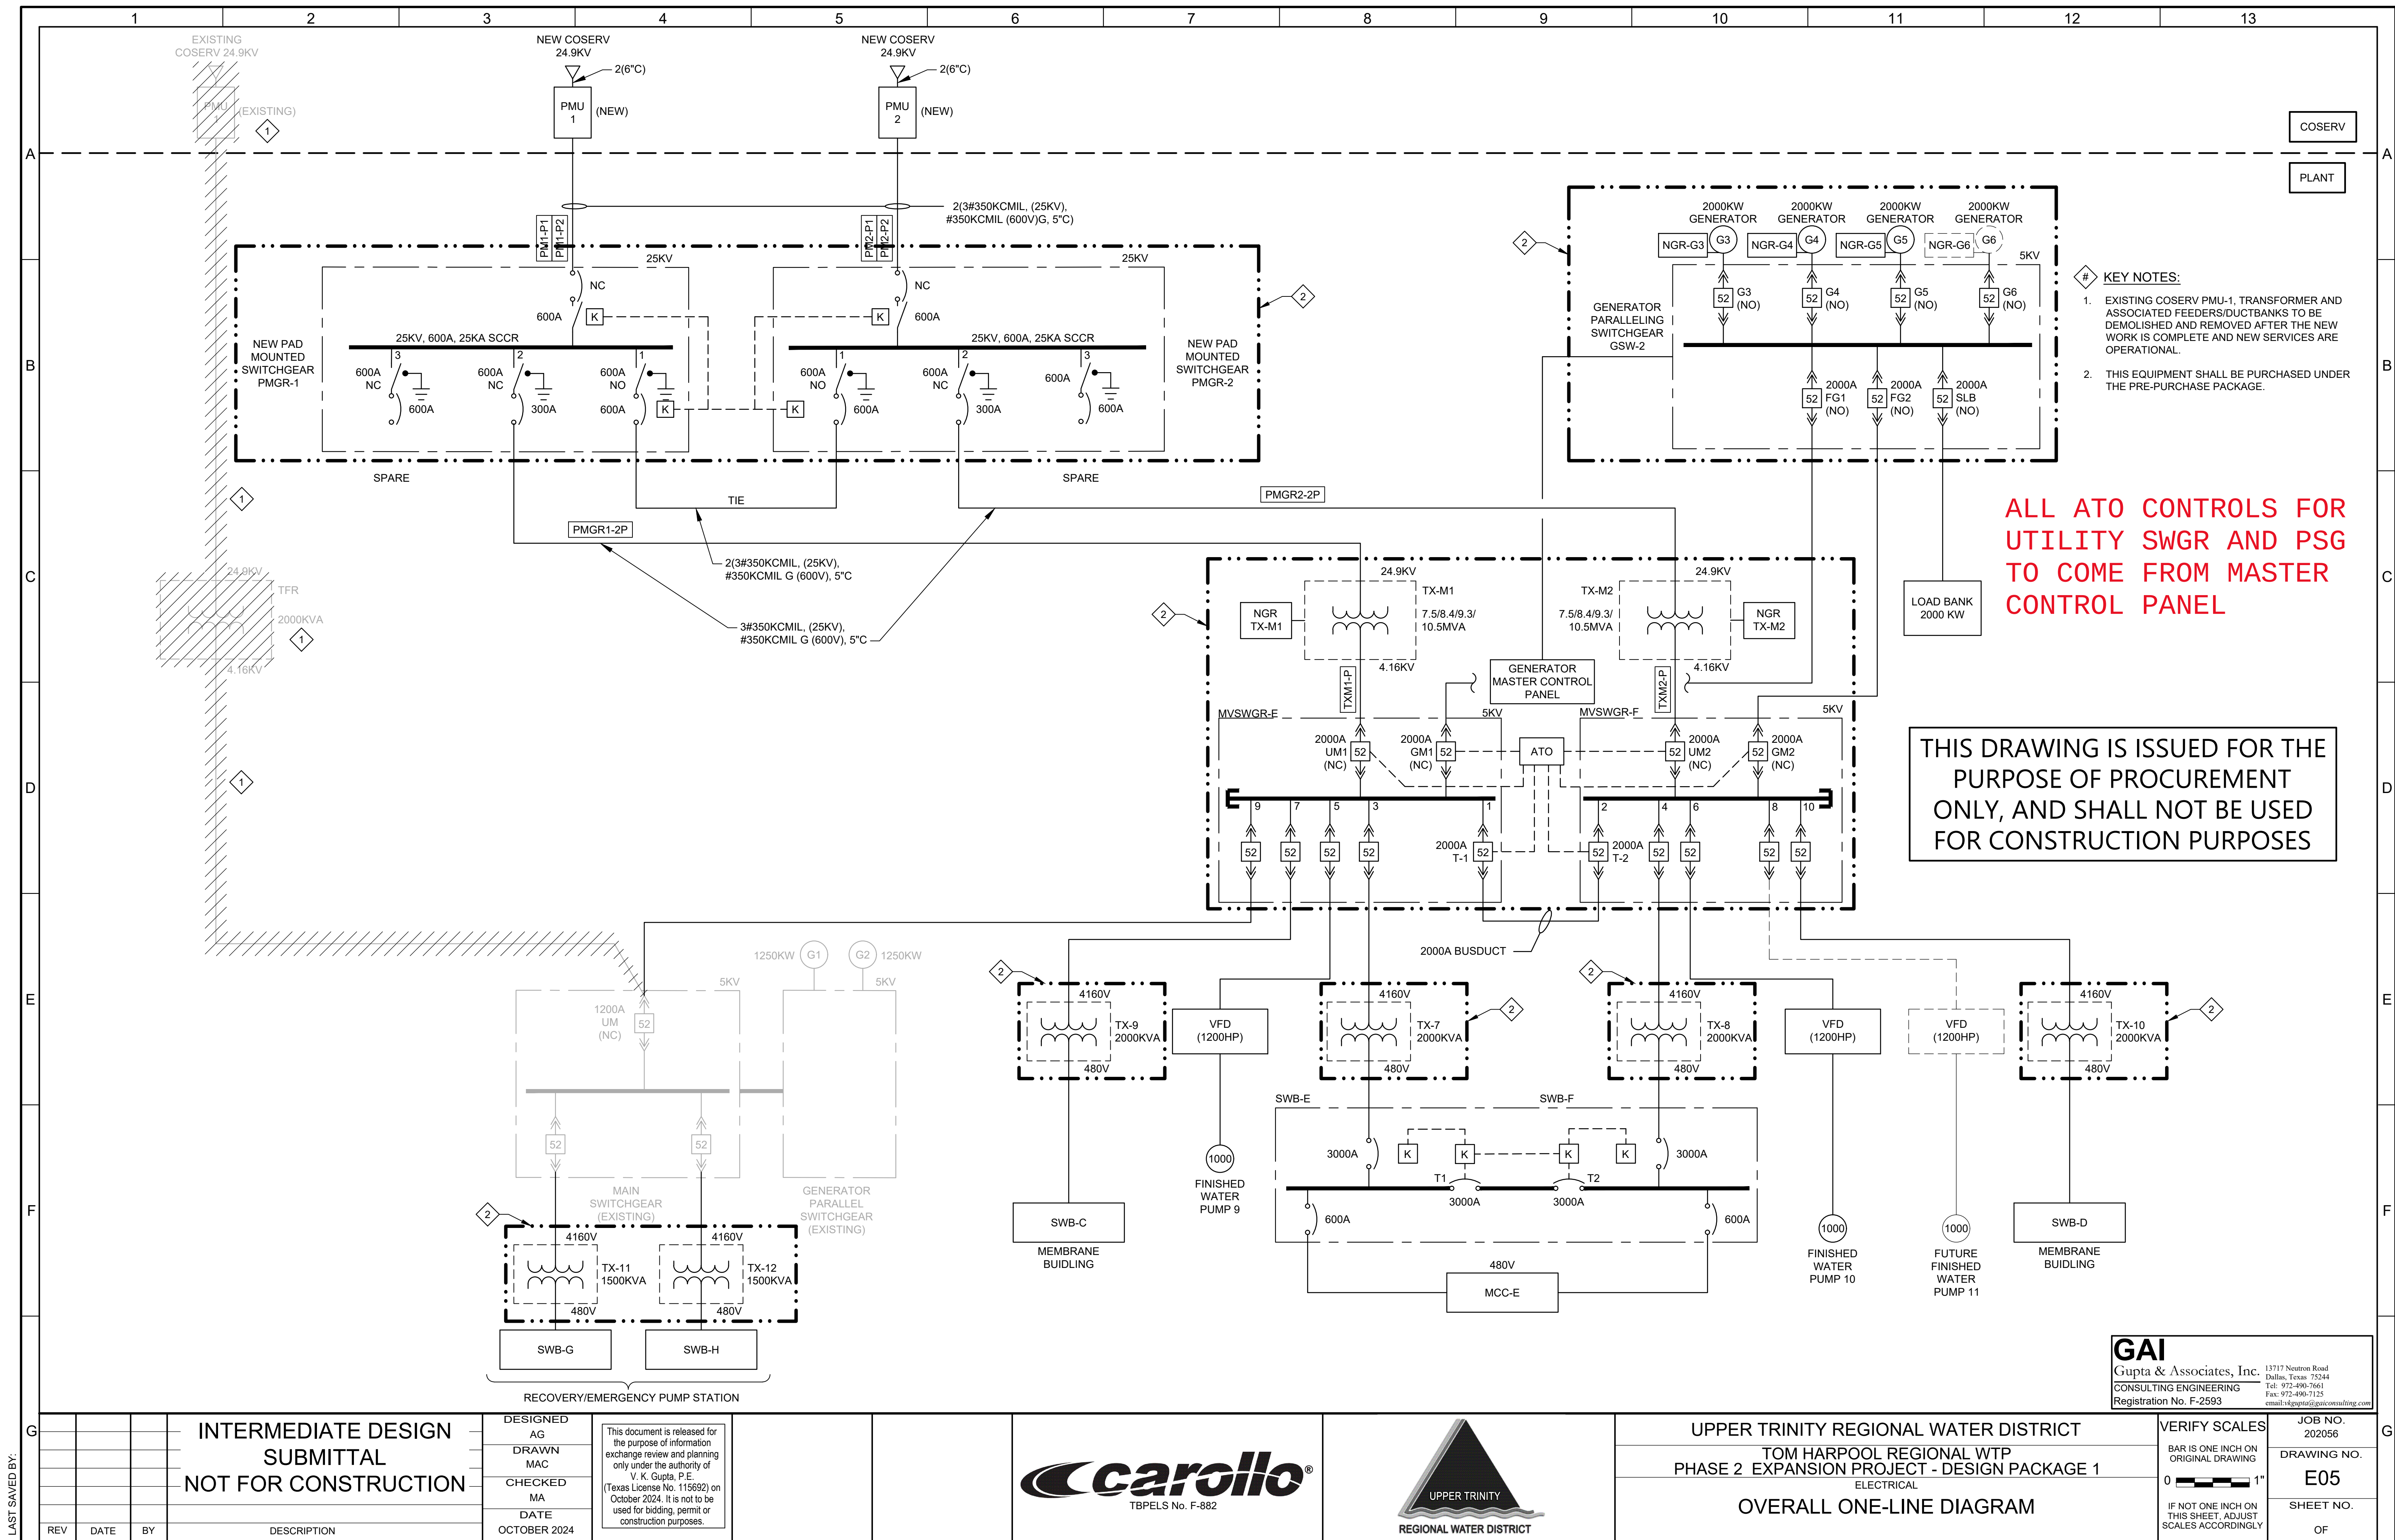

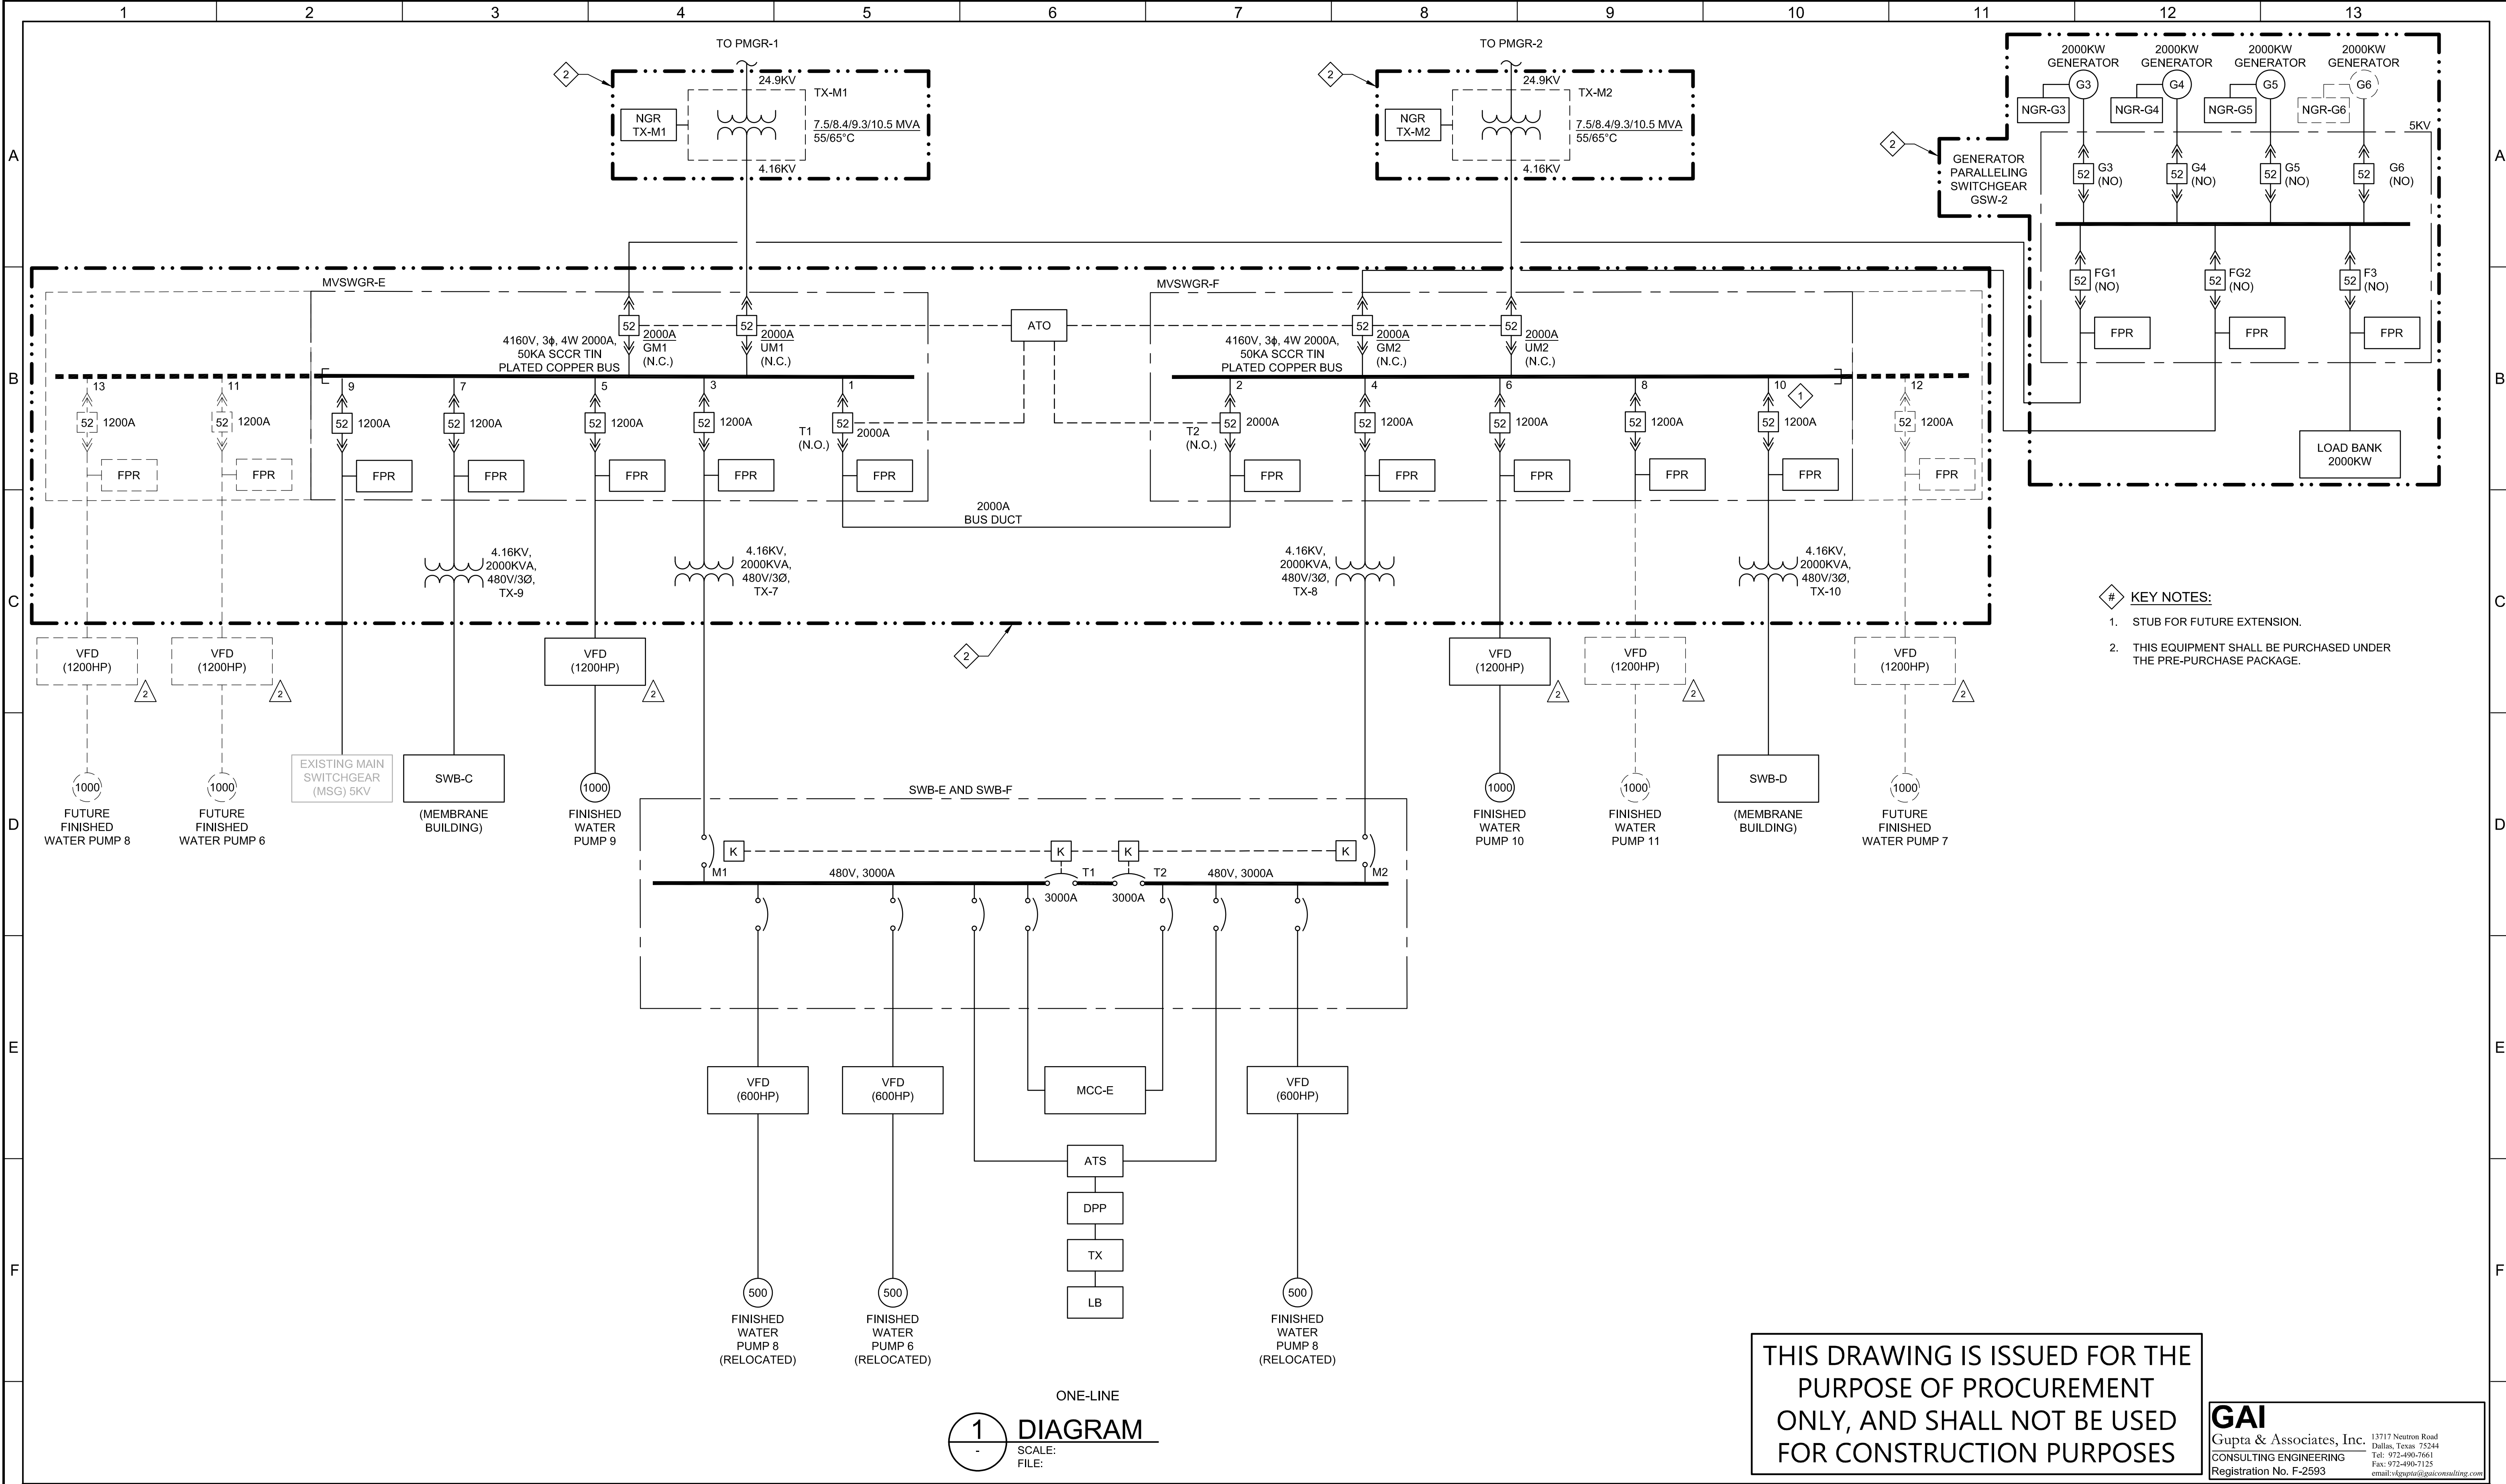

ONE-LINE
1 DIAGRAM
SCALE:
FILE:

THIS DRAWING IS ISSUED FOR THE
PURPOSE OF PROCUREMENT
ONLY, AND SHALL NOT BE USED
FOR CONSTRUCTION PURPOSES

GAI
Gupta & Associates, Inc.
CONSULTING ENGINEERING
Registration No. F-2593

13717 Neutron Road
Dallas, Texas 75244
Tel: 972-490-7661
Fax: 972-490-7125
email: vkgupta@gaiconsulting.com

G				INTERMEDIATE DESIGN SUBMITTAL NOT FOR CONSTRUCTION		DESIGNED AG	This document is released for the purpose of information exchange review and planning only under the authority of V. K. Gupta, P.E. (Texas License No. 115692) on October 2024. It is not to be used for bidding, permit or construction purposes.				 TBPELS No. F-882	 REGIONAL WATER DISTRICT	UPPER TRINITY REGIONAL WATER DISTRICT		VERIFY SCALES	JOB NO. 202056	G	
						DRAWN MAC							TOM HARPOOL REGIONAL WTP PHASE 2 EXPANSION PROJECT - DESIGN PACKAGE 1		BAR IS ONE INCH ON ORIGINAL DRAWING	DRAWING NO.		
						CHECKED MA							ELECTRICAL		0  1"	E06		
						DATE OCTOBER 2024							OVERALL PUMP STATION ONE-LINE DIAGRAM		IF NOT ONE INCH ON THIS SHEET, ADJUST SCALES ACCORDINGLY	SHEET NO.		
																OF		

