



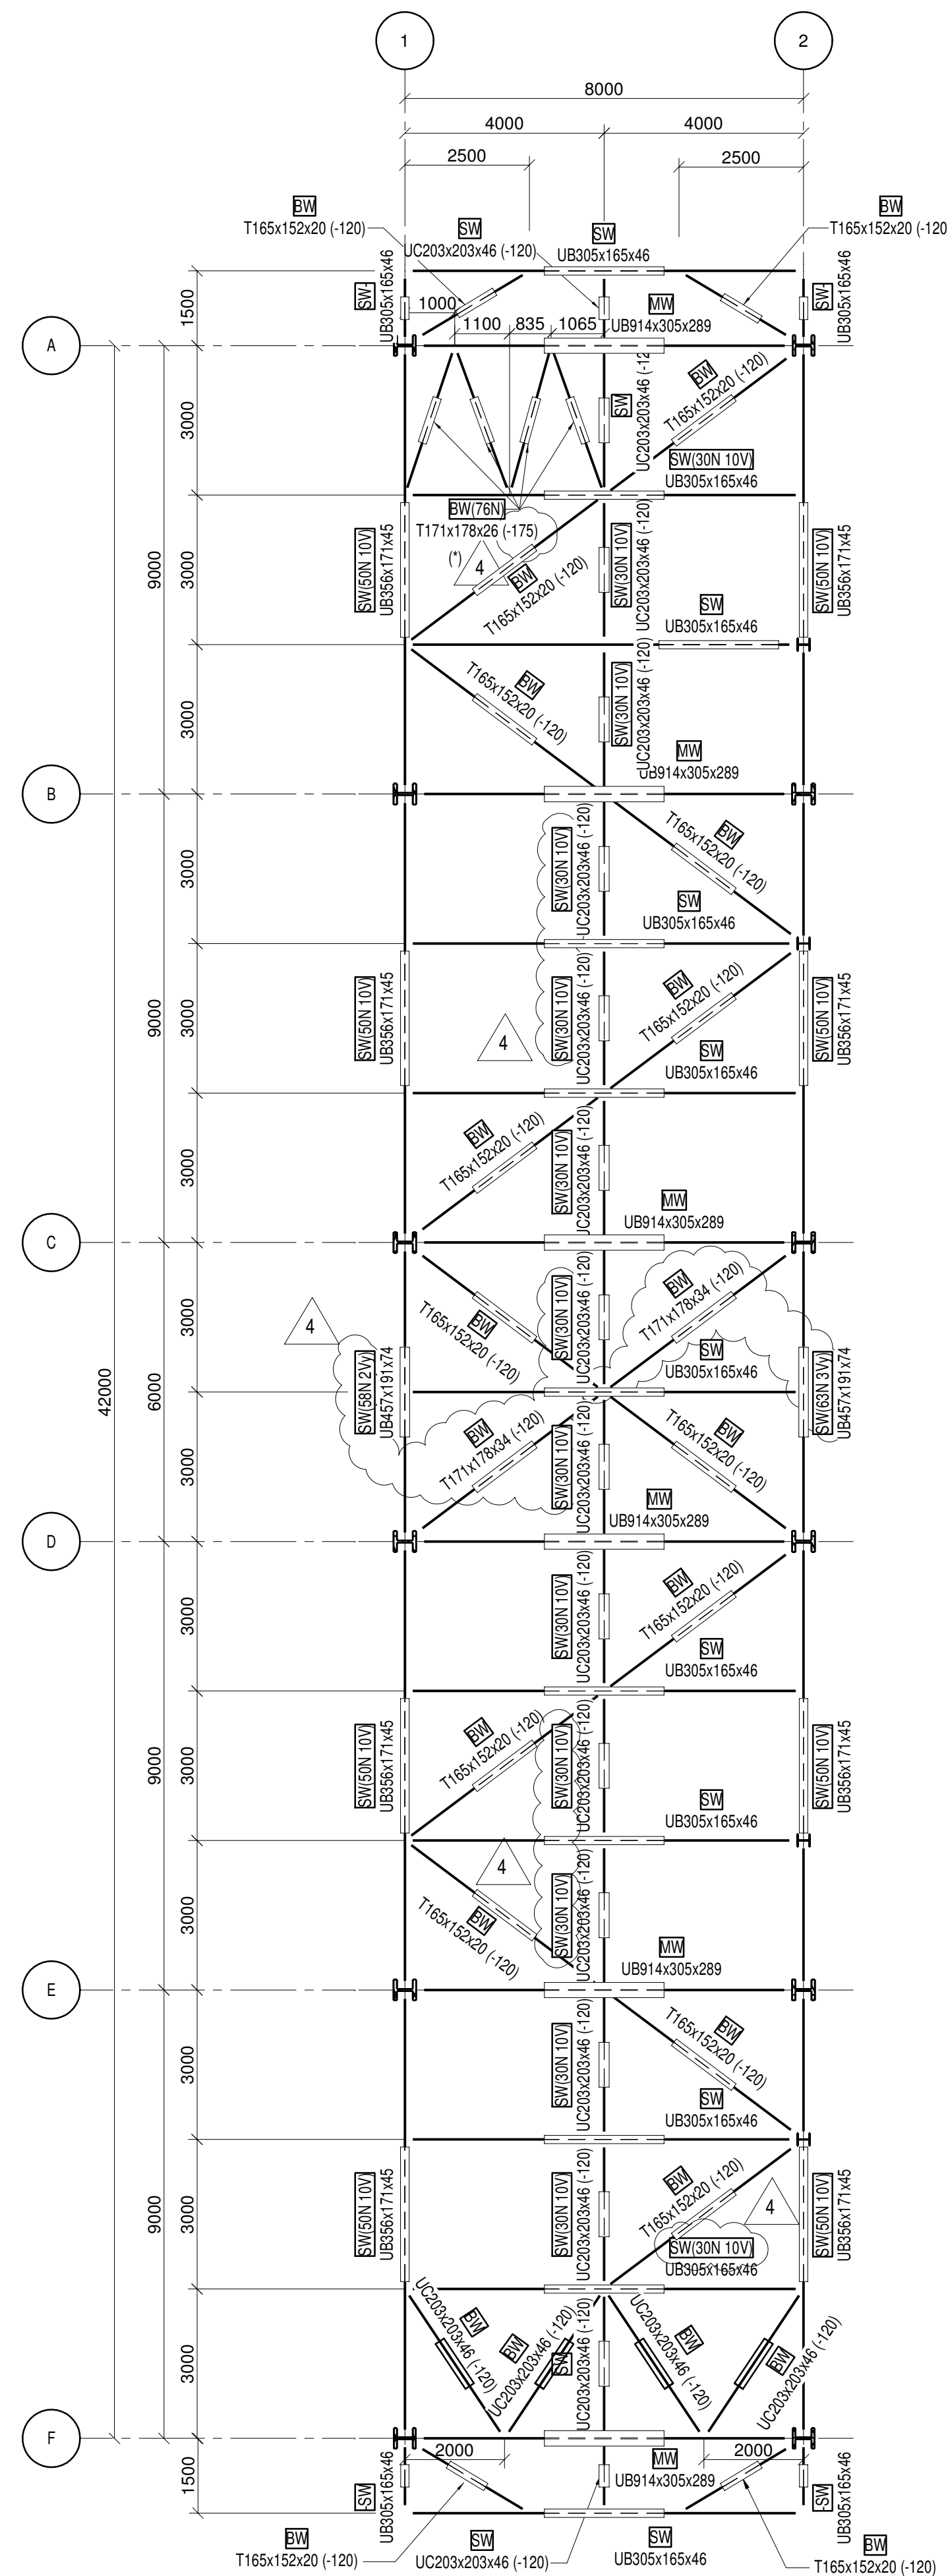

PLAN EL. 111.500 (T.O.S.)
SCALE 1:100

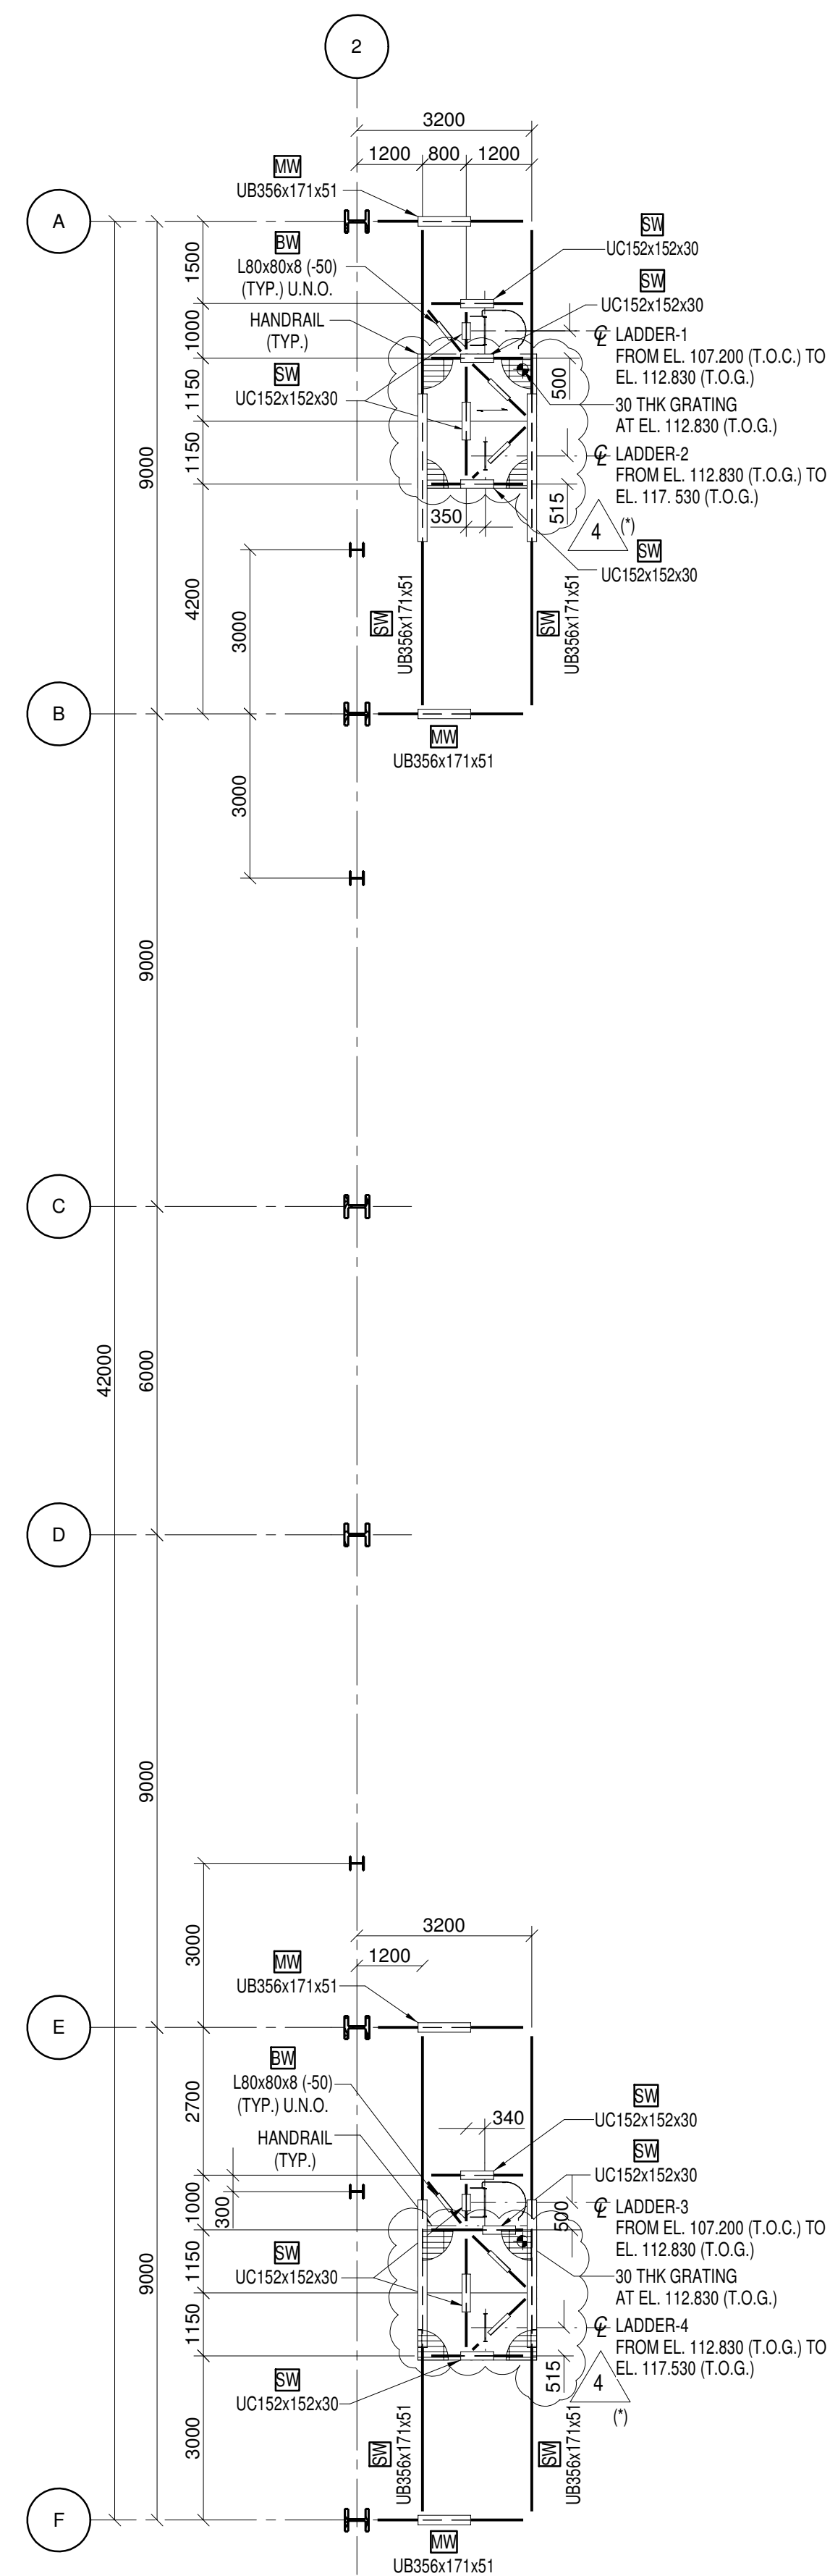

PLAN EL. 112.800 (T.O.S.)
SCALE 1:100

1. FOR GENERAL NOTES, REFERENCES DRAWINGS AND KEYPLAN SEE SHEET 001.

(*) CLOUDS MARKED WITH (*) INDICATE CHANGES THAT HAVE ALREADY BEEN COMMUNICATED TO STEEL STRUCTURE FABRICATOR.

[illegible]

0 1m 2m 4m 6m 8m 10m

SCALE 1:100

			VPM	AVH	CPH	NP	N/A
4	27.07.2026	ISSUED FOR CONSTRUCTION	VPM	AVH	CPH	JFM	MM
3	20.04.2026	ISSUED FOR CONSTRUCTION	VPM	FEN	VVR	NHP	MM
2	04.02.2026	ISSUED FOR APPROVAL	VPM	GMA	VVR	NHP	MM
1	09.01.2026	ISSUED FOR REVIEW	SCC	GMA	VVR	NHP	MM
REV	DATE	DESCRIPTION	BY	CHK	SD	APPD	APPCD

CONSULTANT/CONTRACTOR/VENDOR



TECNICAS REUNIDAS

DRAWING No.	AD-3010-C-330030-SHT-004
-------------	--------------------------

PROJECT/PMR TITLE	LOWER ZAKUM LONG TERM DEVELOPMENT PLAN PHASE-1 (LZ LTDP-1) - EPC WORKS PACKAGE 2
-------------------	---



أدنوك البحرية
ADNOC Offshore

DRAWING TITLE	UTILITIES - UNIT 3010 AL OMAIRAH ISLAND 3010PAR002 STEEL STRUCTURE PLAN EL. 111.500 & 112.800 (T.O.S.)
---------------	---

BUDGET REF. 14001-10222-2		DRAWING No. AD-3010-C-330030-SHT-004	SHT.No.	REV.
PROJ/PMR No. 10222-2	SCALE AS SHOWN		004	4

Filename : AD-3010-C-330030-SHT-004.SHA

THE INFORMATION/DESIGN CONTAINED ON THIS DRAWING IS CONFIDENTIAL. IT MUST NOT BE COPIED, GIVEN AWAY, LENT OR MADE AVAILABLE TO A THIRD PARTY WITHOUT THE WRITTEN CONSENT OF ADNOC Offshore.
ALL THE WORK TO BE CARRIED OUT IN ACCORDANCE WITH THE CONTRACT SPECIFICATION. EXPLANATIONS OF ABBREVIATIONS, SYMBOLS ETC. ARE GIVEN IN ADNOC Offshore CODES OF PRACTICE.

SHT. SIZE: A1