

LINE TYPES	FLAGS & ABBREVIATIONS	PIPING & INSTRUMENTS SYMBOLS	DESIGNATION CODES	
MAIN PROCESS LINE TO EQUIPMENT MAIN PROCESS LINE WITH STEAM JACKET(CONTINUOUS) UTILITY LINE, BYPASS, & MINOR PROCESS LINE INDICATES FUTURE, EXISTING OR ALTERNATE CASES(LINES & EQUIPMENT) INDICATES PACKAGE OR MODULE BOUNDARIES & BATTERY LIMITS LINE TO ATMOSPHERE LINE TO GRADE ELECTRICAL TRACING STEAM TRACING HOT OIL TRACING SYMBOL WILL BE SHOWN BELOW LINE NUMBER ELECTROMAGNETIC OR SONIC (WITHOUT WIRING OR TUBING) SIGNAL HYDRAULIC SIGNAL PNEUMATIC SIGNAL ELECTRICAL SIGNAL CAPILLARY TUBING SOFTWARE LINK JACKETED LINE INSULATED LINE DIRECTION OF FLOW BRANCH CONNECTION CROSSOVER LINE SIGNAL BRANCH SLOPING LINE, ANGLE NOTED	PIPING CONTINUATION SIGNAL CONTINUATION F FLARE AD ACID DRAIN OD OPEN DRAIN CD CLOSED DRAIN CCD COLD CLOSED DRAIN SD SOLVENT DRAIN SD SOLVENT DRAIN IF MORE THAN ONE SYSTEM WITHIN PLANT GD GLYCOL DRAIN BF BLIND FLANGE CSC CAR SEAL CLOSED CSO CAR SEAL OPEN E EXISTING ESD EMERGENCY SHUTDOWN (F) FINISHED WITH ASSOCIATED EQUIPMENT OR BY OTHERS FC FAIL CLOSED FI FAIL INDETERMINATE FO FAIL OPEN FP FREEZE PROTECTION HC HOSE CONNECTION HOA HAND-OFF-AUTOMATIC I.A.S. INSTRUMENT AIR SUPPLY I.G.S. INSTRUMENT GAS SUPPLY L.O. LOCK CLOSED L.C. LOCK OPEN MCC MOTOR CONTROL CENTER NO NORMALLY OPEN NC NORMALLY CLOSED NT NORMALLY THROTTLED PP PERSONNEL PROTECTION PPE PREFERRED PRESSURE END PT PRESSURE TAP R REUSED SC SAMPLE CONNECTION S/D SHUTDOWN SF SENIOR TYPE FITTING SP SWEET PURGE TS TIGHT SHUTOFF VB VORTEX BREAKER	BREAKOUT FLANGES BLIND FLANGE OR LINE TERMINATION LINE BLIND OPEN LINE BLIND CLOSED OPEN FIGURE 8 (SPECTACLE) BLIND CLOSED FIGURE 8 (SPECTACLE) BLIND ANGLE VALVE GATE VALVE BALL VALVE GLOBE VALVE PLUG VALVE PLUGGED OR BLINDED VALVE 3-WAY VALVE 4-WAY VALVE BUTTERFLY VALVE CHECK VALVE CHOKE VALVE DIAPHRAGM VALVE NEEDLE VALVE TIE-IN LOCATION SAMPLE CONNECTION OR PLUG LINE SIZE CHANGE CLEANOUT CONNECTION CONICAL BASKET OR TEMPORARY TYPE STRAINER CORROSION COUPON GAUGE VALVE WITH BLEEDER DESICCANT FLAME ARRESTOR CHEMICAL SEAL STEAM JACKETED VALVE STEAM SUPPLY &COND. RETURN W/TRAP REQUIRED TEST RING LUBRICATOR PROCESS TRAP STEAM TRAP "Y" TYPE STRAINER "T" TYPE STRAINER HOSE CONNECTION FLEXIBLE HOSE SPRAY NOZZLE EXPANSION JOINT SPECIALTY ITEM SPECIFICATION CHANGE OR RESPONSIBILITY BREAK EQUIPMENT INSULATION PULSATION DAMPENER VENT VENT WITH BUG SCREEN STATIC MIXER PIPE CAP DEMISTER SIPHON BLOW-OFF SACRIFICIAL ANODE TANDEM SEAL	SERVICE IDENTIFICATION CODE SERVICE AD ATMOSPHERIC DRAIN AM AMINE C CONDENSATE CH CHEMICAL CD CARBON DIOXIDE CW COOLING WATER D DIESEL FUEL DC DRY CHEMICAL EX ENGINE EXHAUST FG FUEL GAS FW FIREWATER G GAS GL GLYCOL HM HEAT MEDIA HO HYDRAULIC OIL HV HIGH PRESSURE VENT IA INSTRUMENT AIR IG INSTRUMENT GAS JW JACKET WATER LO LUBE OIL LV LOW PRESSURE VENT N NITROGEN NG NATURAL GAS LIQUIDS OD OPEN DRAIN PD PROCESS DRAIN PF PRODUCED FLUIDS PO PRODUCED OIL PW POTABLE WATER RP REFRIGERANT PROPANE S STEAM SC STEAM CONDENSATE SO SEAL OIL SW SEAWATER UA UTILITY AIR UG UTILITY GAS W WATER (PRODUCED) WS SEWAGE WATER (BLACK) TYPICAL LINE NUMBER 6"-PO-0001-A3-1.5"H-EL LINE SIZE (INCHES) SERVICE IDENTIFICATION LINE NUMBER (3 DIGITS REQ'D) CLASS CODE INSULATION THICKNESS(INCHES) INSULATION TYPE HC - HEAT CONSERVATION CC - COLD CONSERVATION PP - PERSONAL PROTECTION AC - ACOUTIC CLADDING CS - CALCIUM SILICON FG - FOAM GLASS HEAT TRACE TYPE TYPICAL SPECIALTY ITEM NUMBER SP 001 ITEM NUMBER	PIPING SYSTEM SPECIFICATION CLASS CODE FLANGE RATING MATERIAL CORROSION ALLOWANCE BRANCH CONN. TABLE A ANSI - 150 RF Carbon Steel 1/16" F A1 ANSI - 150 RF Carbon Steel 1/8" K A2 ANSI - 150 RF Carbon Steel (Low Temp.) 1/16" K A3 ANSI - 150 RF Carbon Steel (LP Steam) 1/16" F A4 ANSI - 150 RF Carbon Steel (NACE) 1/16" G A5 ANSI - 150 RF Carbon Steel (NACE) 1/8" G B ANSI - 300 RF Carbon Steel 1/16" F B1 ANSI - 300 RF Carbon Steel 1/8" K B2 ANSI - 300 RF Carbon Steel (Low Temp.) 1/16" K B3 ANSI - 300 RF Carbon Steel (NACE) 1/16" G B4 ANSI - 300 RF Carbon Steel (NACE) 1/8" G C (Not Used) ANSI - 400 D ANSI - 600 RF Carbon Steel 1/16" F D1 ANSI - 600 RF Carbon Steel 1/8" K D2 ANSI - 600 RF Carbon Steel (Low Temp.) 1/16" K D3 ANSI - 600 RF Carbon Steel (NACE) 1/8" G E ANSI - 900 RTJ Carbon Steel 1/16" F E1 ANSI - 900 RTJ Carbon Steel 1/8" K F ANSI - 1500 RTJ Carbon Steel 1/16" F F1 ANSI - 1500 RTJ Carbon Steel (NACE) 1/16" G F6 ANSI - 1500 RF Forged Steel (NACE)INJ. COMP 1/16" D G ANSI - 2500 RTJ Carbon Steel 1/16" F H (Not Used) API - 2000 J API - 3000 RTJ Carbon Steel 1/16" F K API - 5000 RTJ Carbon Steel 1/16" F L API - 10000 RTJ Carbon Steel 1/16" L M API - 15000 RTJ Carbon Steel 1/16" L N ANSI - 150 FF/RF Fiberglass (FRP) 0" H,I P ANSI - 150 FF CPVC 0" J R ANSI - 150 RF 304 Stainless Steel 0" F S ANSI - 600 RF 304 Stainless Steel 0" F T ANSI - 150 RF Carbon Steel (Galvanized) 1/16" F,H TYPICAL EQUIPMENT NUMBER EQUIPMENT IDENTIFIER E-001 ITEM NUMBER A AGITATOR, MIXER G GENERATOR T ATMOSPHERE TANK B BOILER H HEATER, FURNACE, ETC. U PACKAGED UNIT C COMPRESSOR, FAN, BLOWER, ETC. K COOLING TOWER V PRESSURE VESSEL D DRIVER(TURBINE, MOTOR, ETC.) L ELEVATOR, CONVEYOR W WEIGHING DEVICE, SCALE E HEAT EXCHANGER M CRUSHING & GRINDING X MISCELLANEOUS F FILTER P PUMP R REACTOR FS FLARE STACK S WAG SKID	
3S Services, LLC ENGINEERING & CONSTRUCTION PH: 432-667-5611 Midland, Texas 79705 WWW.3SSERVICES.COM TBPE FIRM REG. #13809 NM FIRM REG. #4545320 OKLA FIRM REG. #3712353615	<table><tr><th>NO.</th><th>DATE</th><th>REVISION</th><th>DRW.</th><th>DES.</th><th>CHK.</th><th>APP.</th></tr><tr><td>A</td><td>05/29/26</td><td>ISSUED FOR APPROVAL</td><td></td><td></td><td></td><td></td></tr><tr><td>B</td><td>06/01/26</td><td>ISSUED FOR APPROVAL</td><td></td><td></td><td></td><td></td></tr></table>	NO.	DATE	REVISION	DRW.	DES.	CHK.	APP.	A	05/29/26	ISSUED FOR APPROVAL					B	06/01/26	ISSUED FOR APPROVAL					<table><tr><th>NO.</th><th>DATE</th><th>REVISION</th><th>DRW.</th><th>DES.</th><th>CHK.</th><th>APP.</th></tr><tr><td>A</td><td>05/29/26</td><td>ISSUED FOR APPROVAL</td><td></td><td></td><td></td><td></td></tr><tr><td>B</td><td>06/01/26</td><td>ISSUED FOR APPROVAL</td><td></td><td></td><td></td><td></td></tr></table>	NO.	DATE	REVISION	DRW.	DES.	CHK.	APP.	A	05/29/26	ISSUED FOR APPROVAL					B	06/01/26	ISSUED FOR APPROVAL					ISSUED MAY 29, 2026 FOR APPROVAL	PIPING & INSTRUMENTATION	SCALE: NTS AFE: DWG. NO: D-260374-11-LEGEND1 PLOT SCALE: 1=1 LOCATION: REV.
NO.	DATE	REVISION	DRW.	DES.	CHK.	APP.	
A	05/29/26	ISSUED FOR APPROVAL	
B	06/01/26	ISSUED FOR APPROVAL	
NO.	DATE	REVISION	DRW.	DES.	CHK.	APP.	
A	05/29/26	ISSUED FOR APPROVAL	
B	06/01/26	ISSUED FOR APPROVAL	

1

2

3


4

A

B

C

D

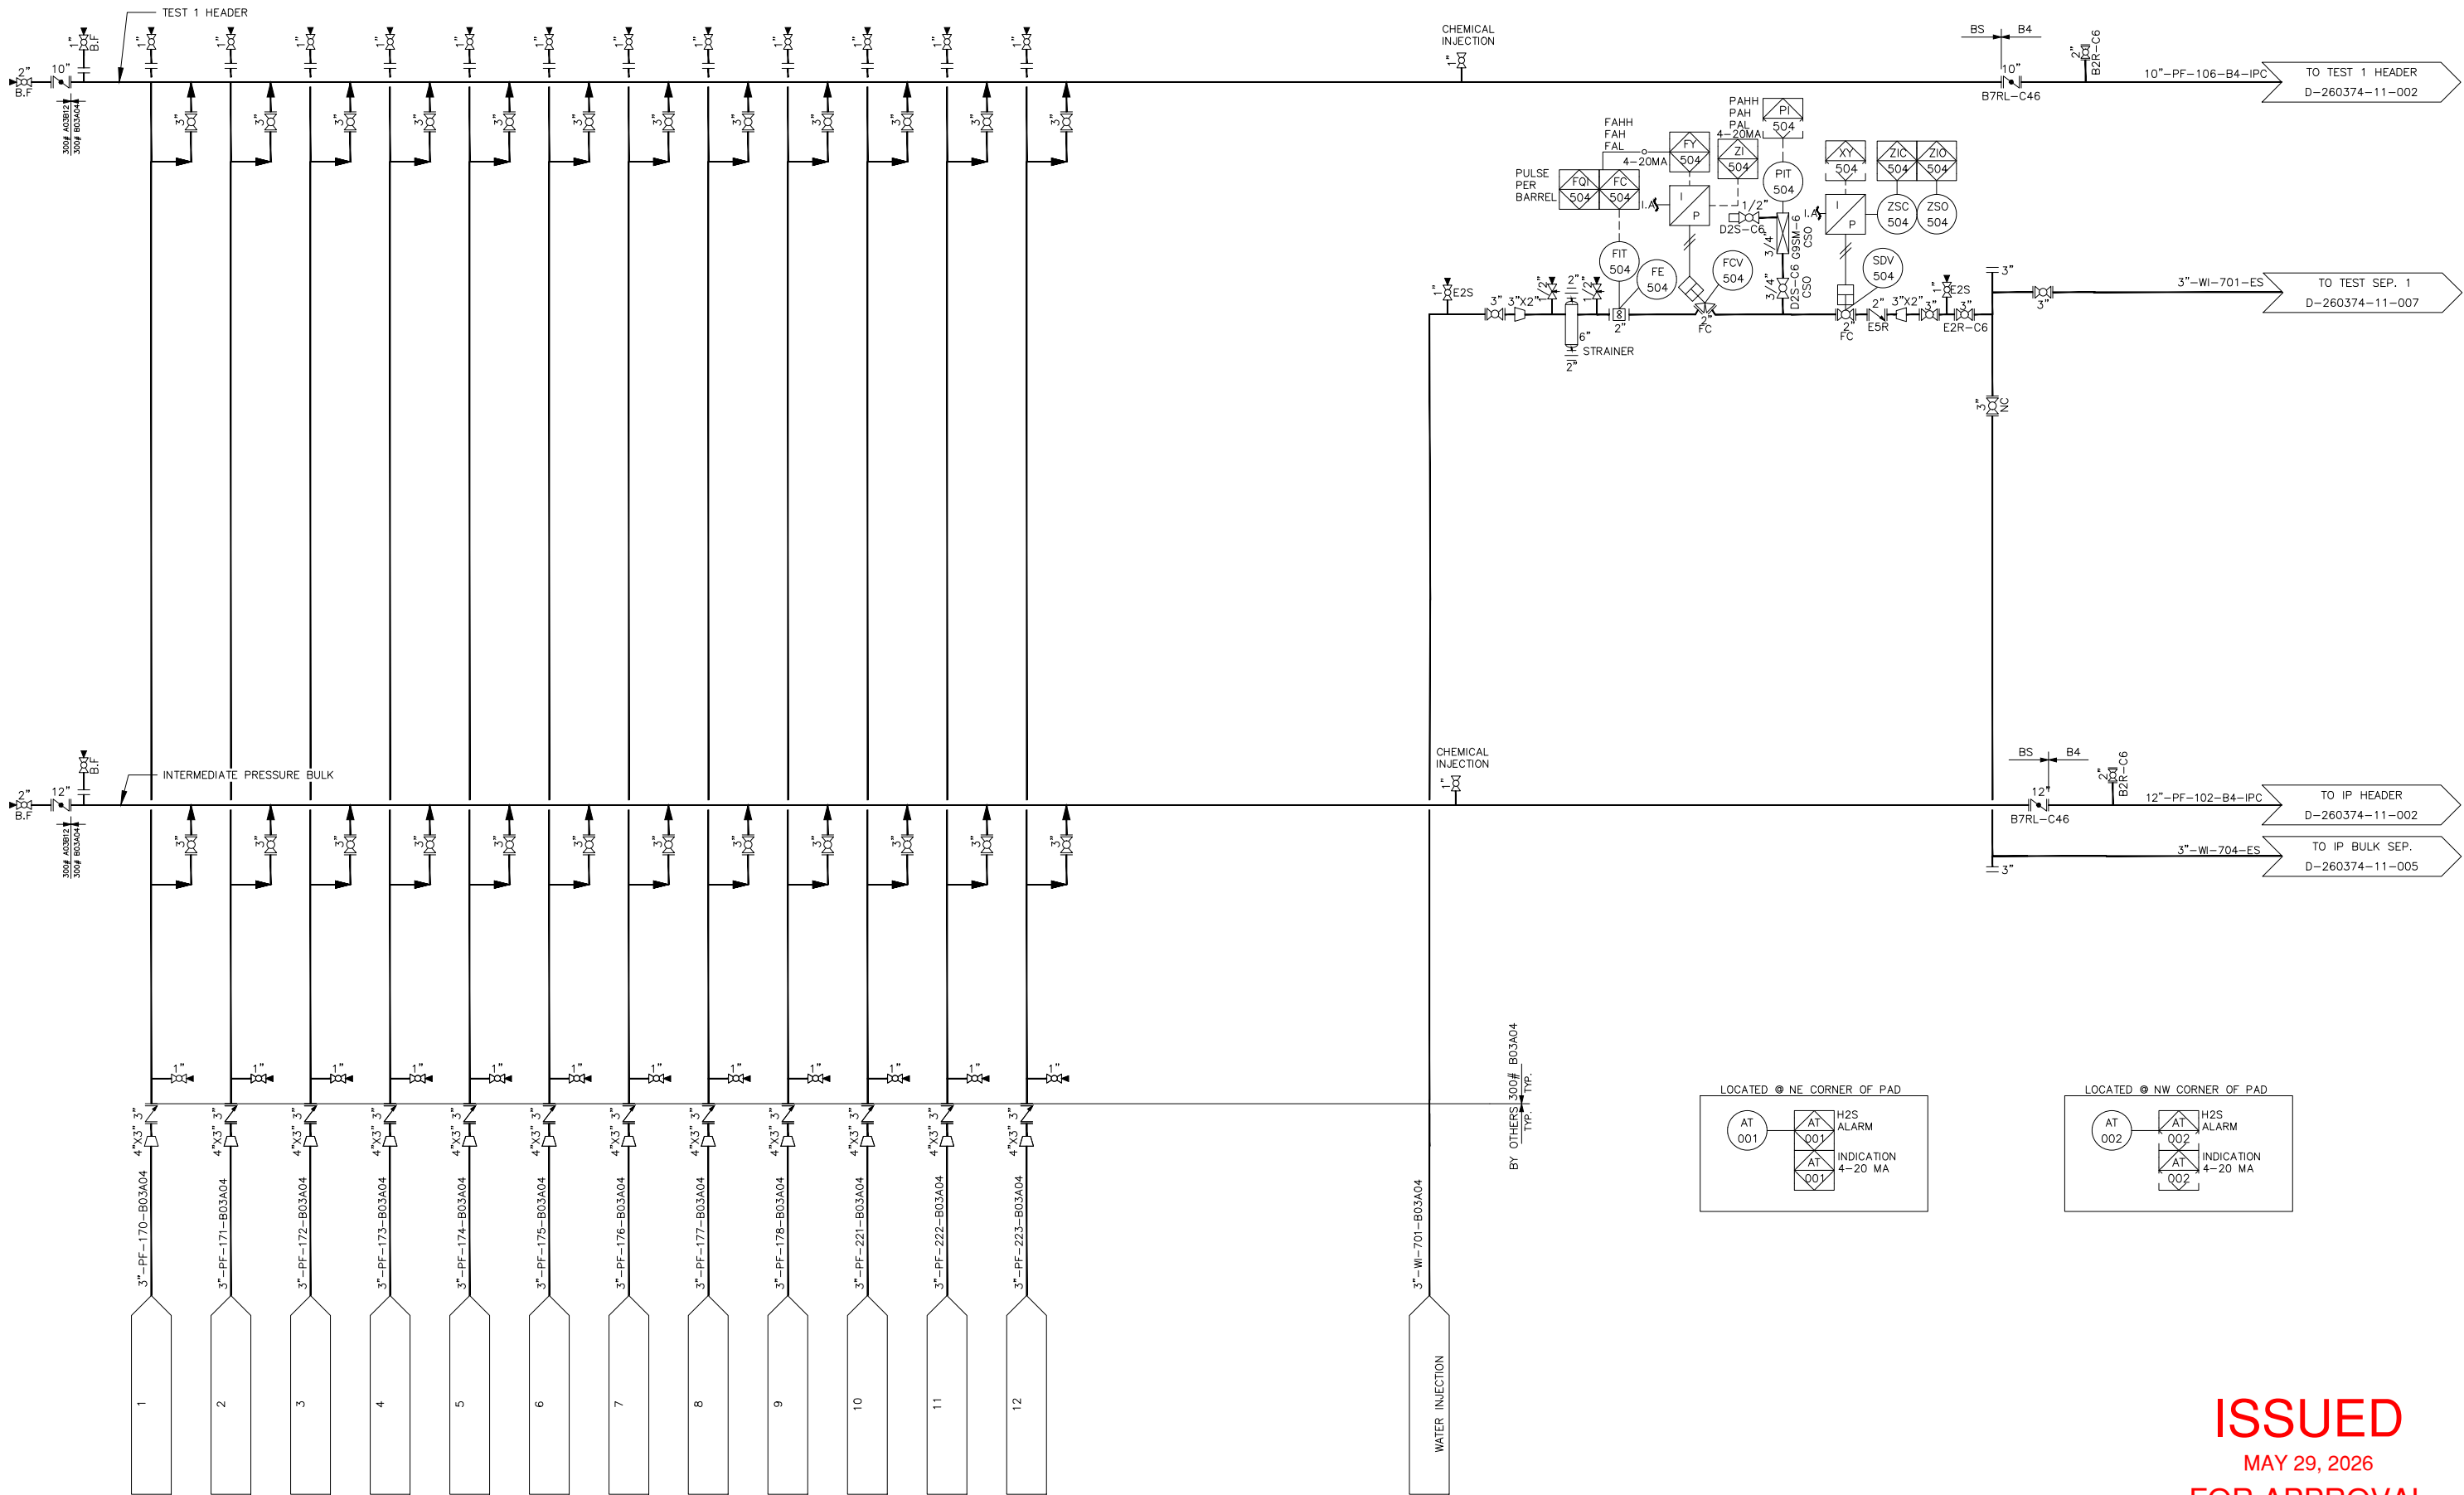


NO.	DATE	REVISION	DRW.	DES.	CHK.	APP.	NO.	DATE	REVISION	DRW.	DES.	CHK.	APP.
							A	05/29/26	ISSUED FOR APPROVAL				
							B	06/01/26	ISSUED FOR APPROVAL				

PIPING & INSTRUMENTATION

ISSUED
MAY 29, 2026
FOR APPROVAL

SCALE: NTS	PLOT SCALE: 1=1
AFE:	LOCATION:
DWG. NO: D-260374-11-001	REV. B

DWG NO.

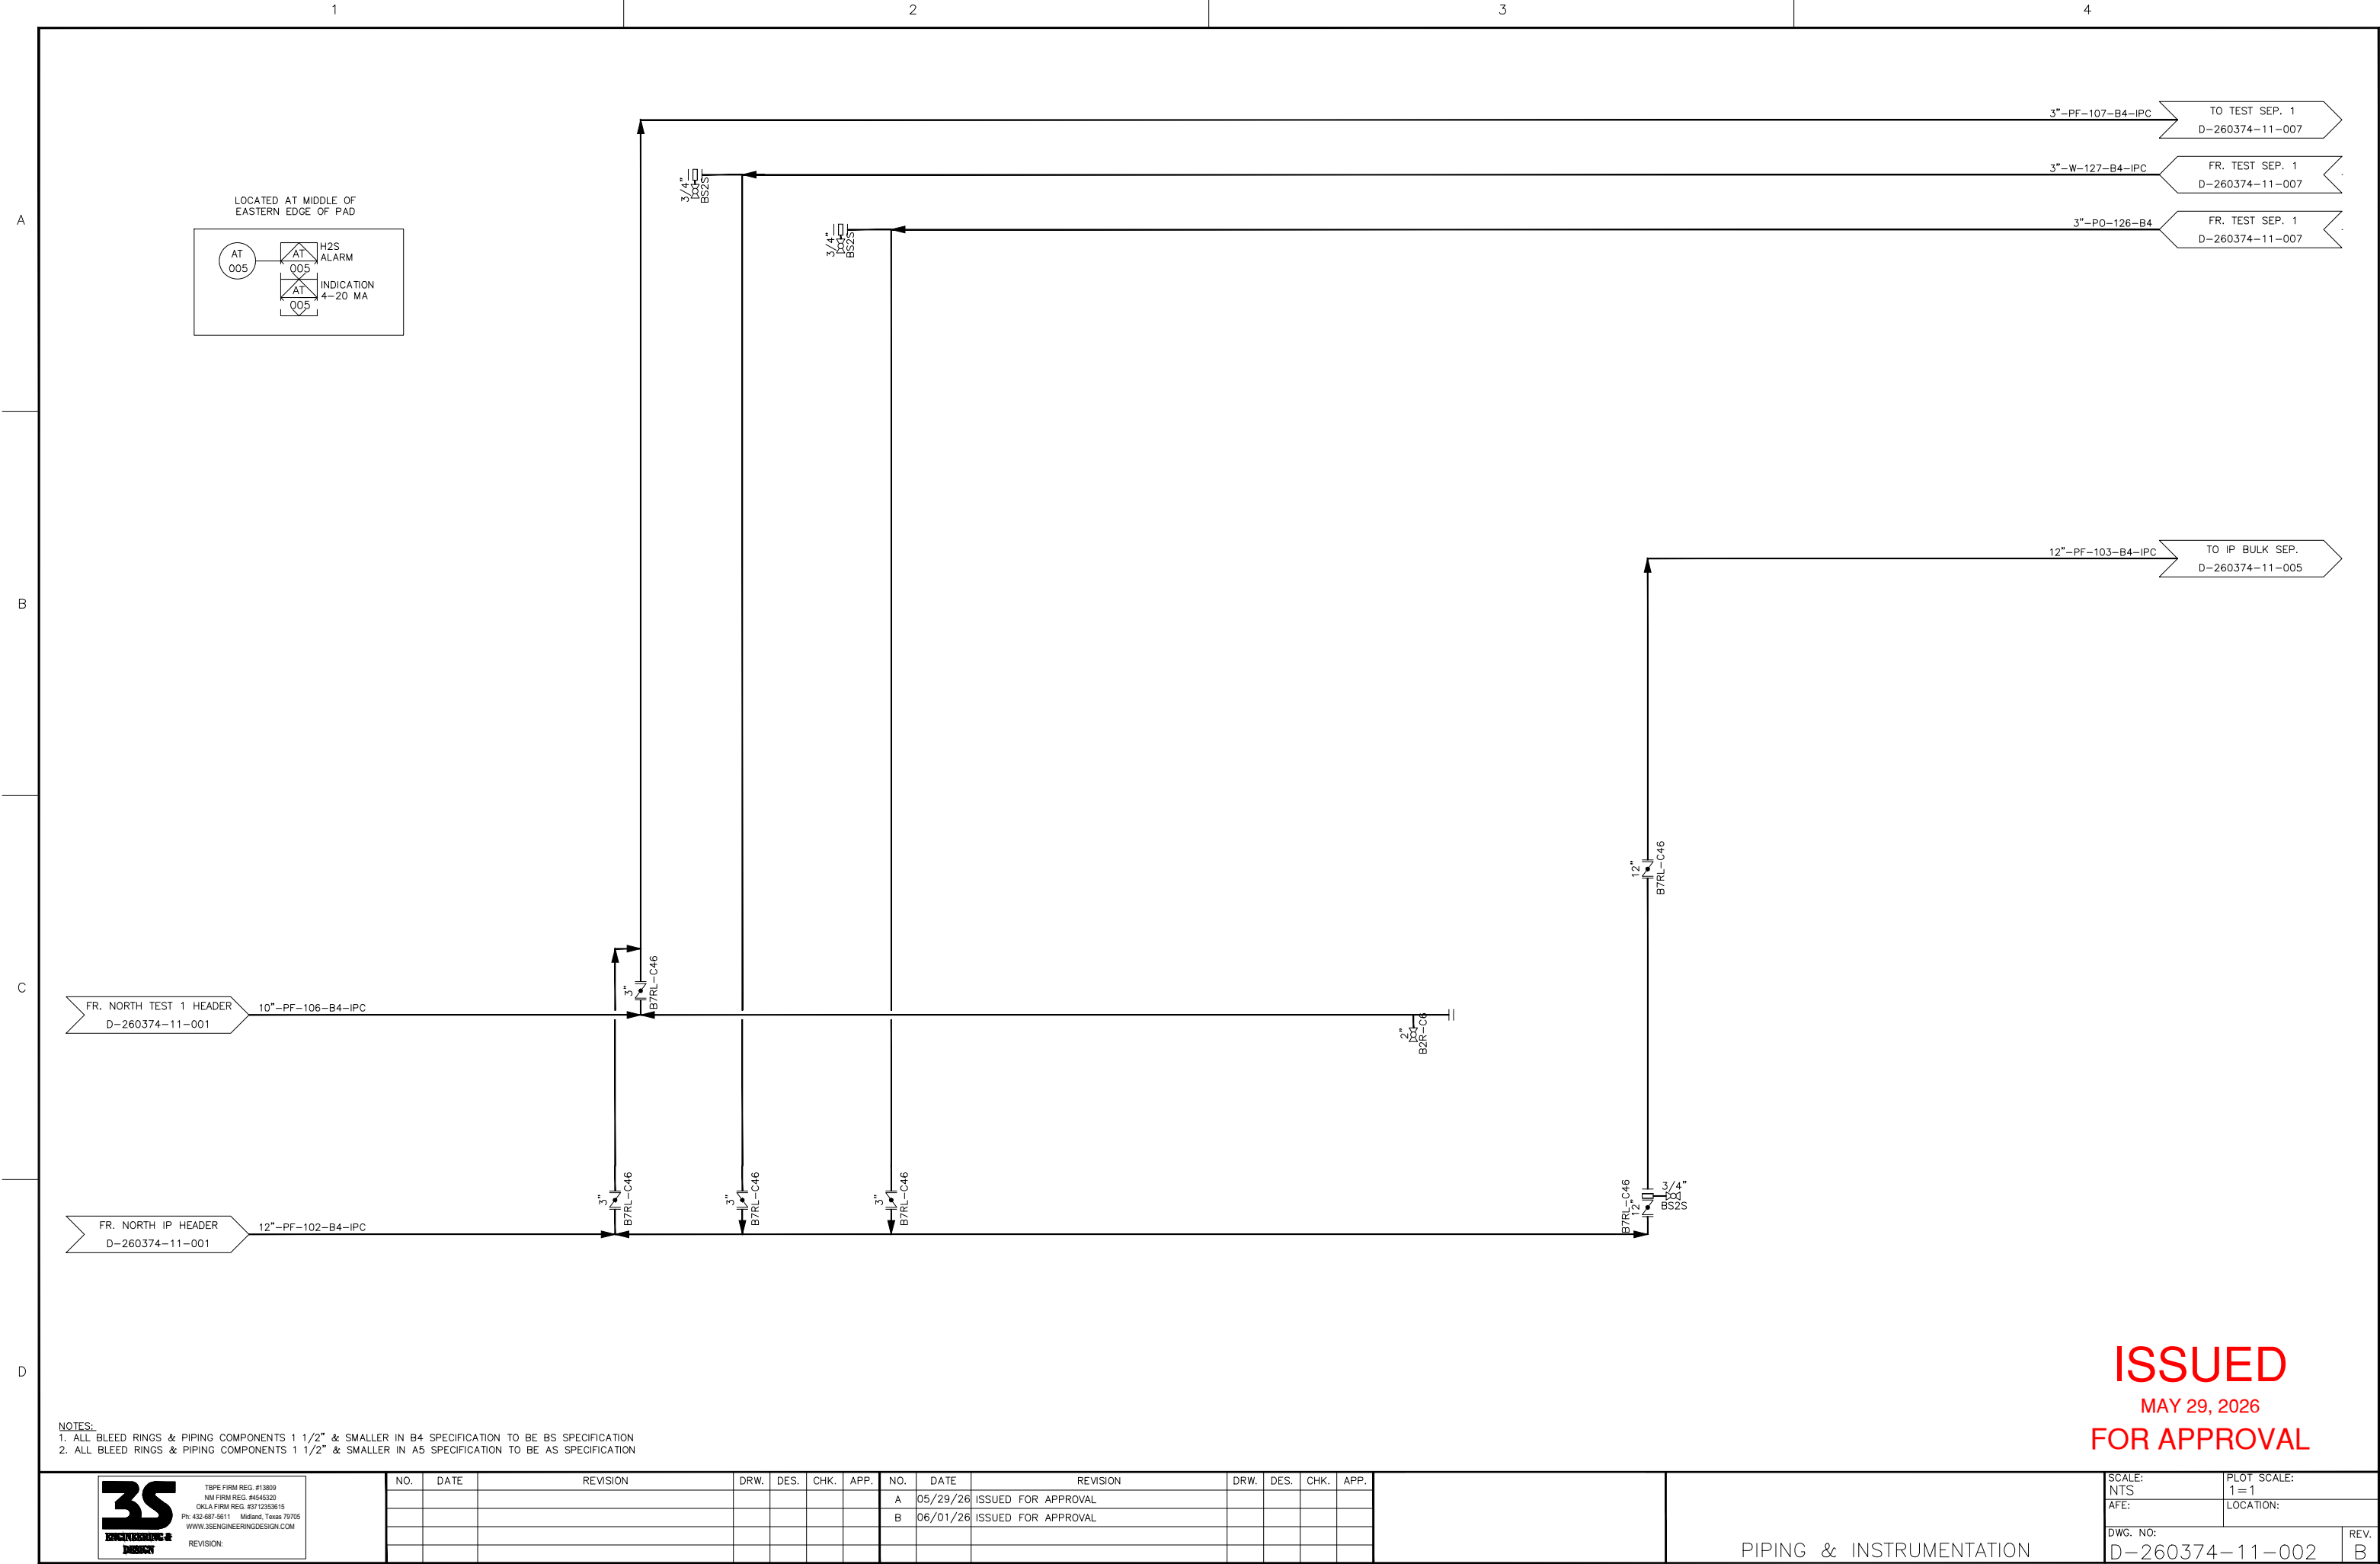

1

2

3

4

A

B

C

D

INTENTIONALLY BLANK

3S

ENGINEERING & DESIGN

TXPE FIRM REG. #13809
NM FIRM REG. #4545320
OKLA FIRM REG. #3712333615
Ph: 432-687-5611 Midland, Texas 79705
WWW.3SENGINEERINGDESIGN.COM

REVISION:

NO.	DATE	REVISION	DRW.	DES.	CHK.	APP.	NO.	DATE	REVISION	DRW.	DES.	CHK.	APP.
							A	05/29/26	ISSUED FOR APPROVAL				
							B	06/01/26	ISSUED FOR APPROVAL				

PIPING & INSTRUMENTATION


SCALE: NTS	PLOT SCALE: 1 = 1
AFE:	LOCATION:
DWG. NO: D-260374-11-003	REV. B

DWG NO.

V-200 INTERMEDIATE PRESSURE BULK SEPARATOR

SIZE: 72" ID X 18'-0" S/S
DESIGN PRESSURE: 345 PSIG @ 200 F
OPERATING PRESSURE: 250 PSIG
MAWP: 345 PSIG @ 200 F

HOLD FOR INFO

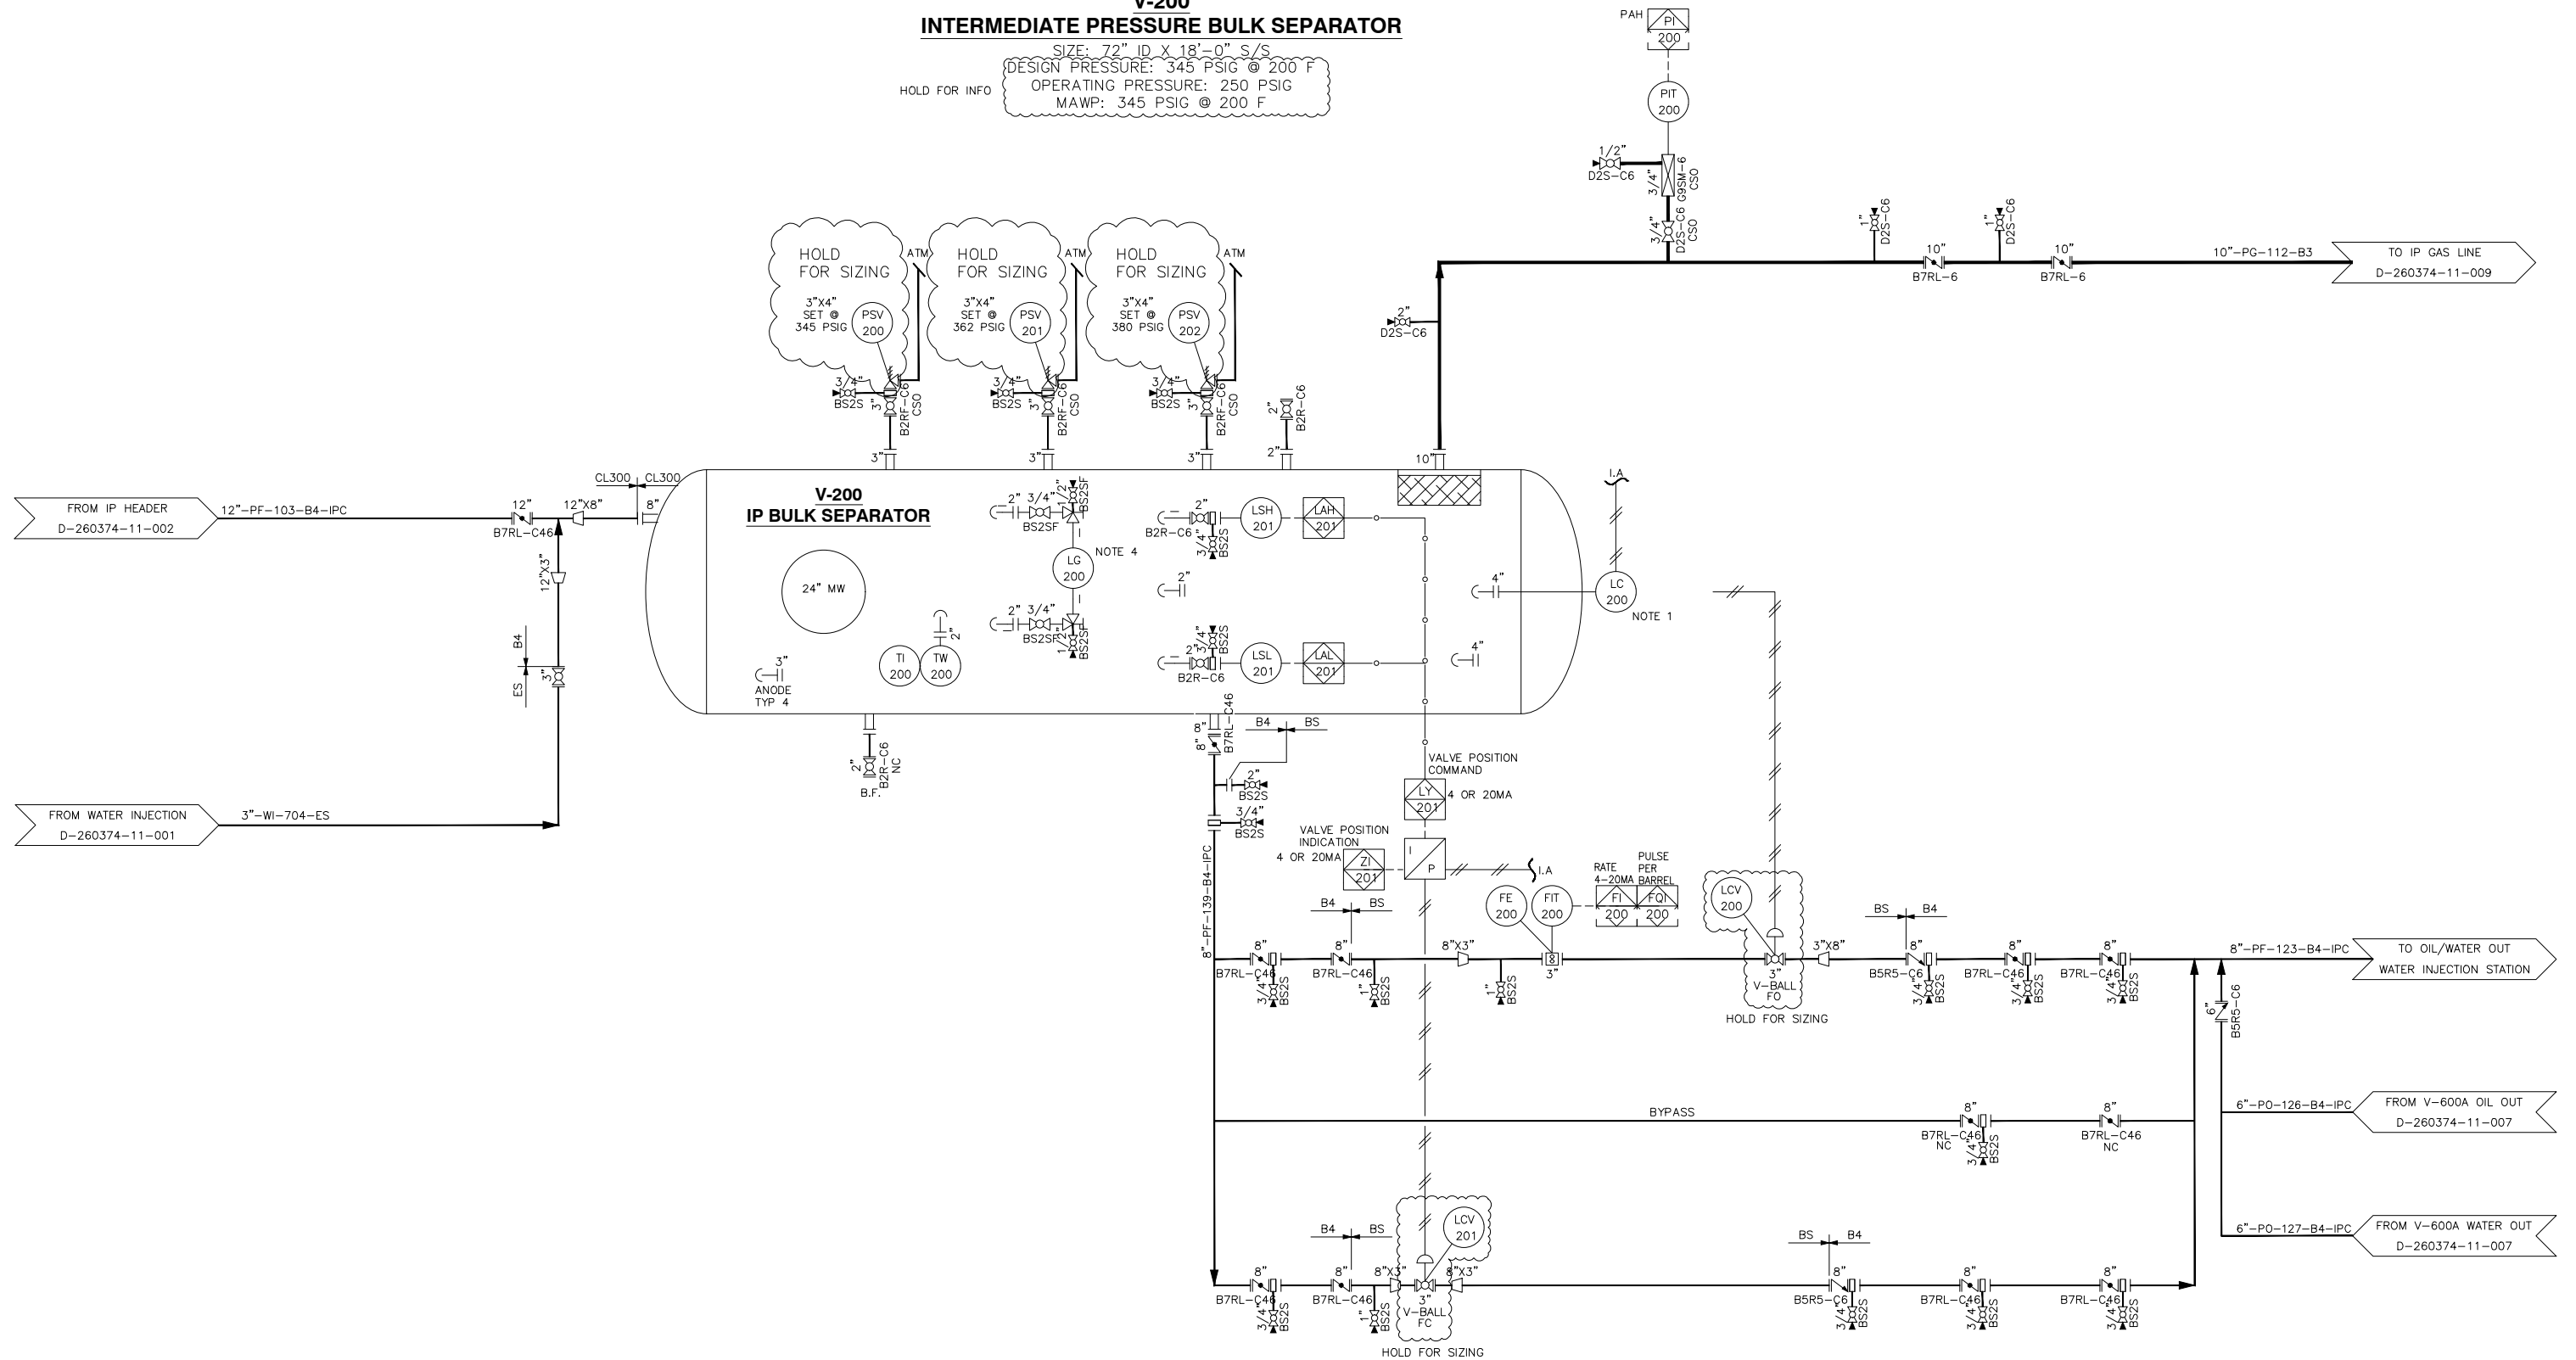

NOTES:

1. INVALCO FLEXTUBE CONTROLLER.
2. ALL BLEED RINGS & PIPING COMPONENTS 1 1/2" & SMALLER IN B4 SPECIFICATION TO BE BS SPECIFICATION
3. ALL BLEED RINGS & PIPING COMPONENTS 1 1/2" & SMALLER IN A5 SPECIFICATION TO BE AS SPECIFICATION
4. LEVEL GAUGE INSULATION TO BE BLANKET TYPE.



REVISION:

NO.	DATE	REVISION	DRW.	DES.	CHK.	APP.	NO.	DATE	REVISION	DRW.	DES.	CHK.	APP.
							A	05/29/26	ISSUED FOR APPROVAL				
							B	06/01/26	ISSUED FOR APPROVAL				

PIPING & INSTRUMENTATION

ISSUED
MAY 29, 2026
FOR APPROVAL

SCALE: NTS	PLOT SCALE: 1=1
AFE:	LOCATION:
DWG. NO: D-260374-11-005	REV. B

DWG NO.

1

2

3

4

A

B

C

D

INTENTIONALLY BLANK



TBPE FIRM REG. #15809
NM FIRM REG. #454320
OKLA FIRM REG. #3712353615
Ph: 432-687-5611 Midland, Texas 79705
WWW.3SENGINEERINGDESIGN.COM

REVISION:

NO.	DATE	REVISION	DRW.	DES.	CHK.	APP.

NO.	DATE	REVISION	DRW.	DES.	CHK.	APP.
A	05/29/26	ISSUED FOR APPROVAL				
B	06/01/26	ISSUED FOR APPROVAL				

PIPING & INSTRUMENTATION

SCALE: NTS	PLOT SCALE: 1=1
AFE:	LOCATION:
DWG. NO: D-260374-11-006	REV. B

DWG NO.

1

2

3

4

A

B

C

D

INTENTIONALLY BLANK



TBPE FIRM REG. #13809
NM FIRM REG. #4545320
OKLA FIRM REG. #3712353615
Ph: 432-687-5611 Midland, Texas 79705
WWW.3SENGINEERINGDESIGN.COM

REVISION:

NO.	DATE	REVISION	DRW.	DES.	CHK.	APP.

NO.	DATE	REVISION	DRW.	DES.	CHK.	APP.
A	05/29/26	ISSUED FOR APPROVAL				
B	06/01/26	ISSUED FOR APPROVAL				

PIPING & INSTRUMENTATION

SCALE: NTS	PLOT SCALE: 1 = 1
AFE:	LOCATION:
DWG. NO: D-260374-11-008	REV. B


DWG NO.

A

B

C

D

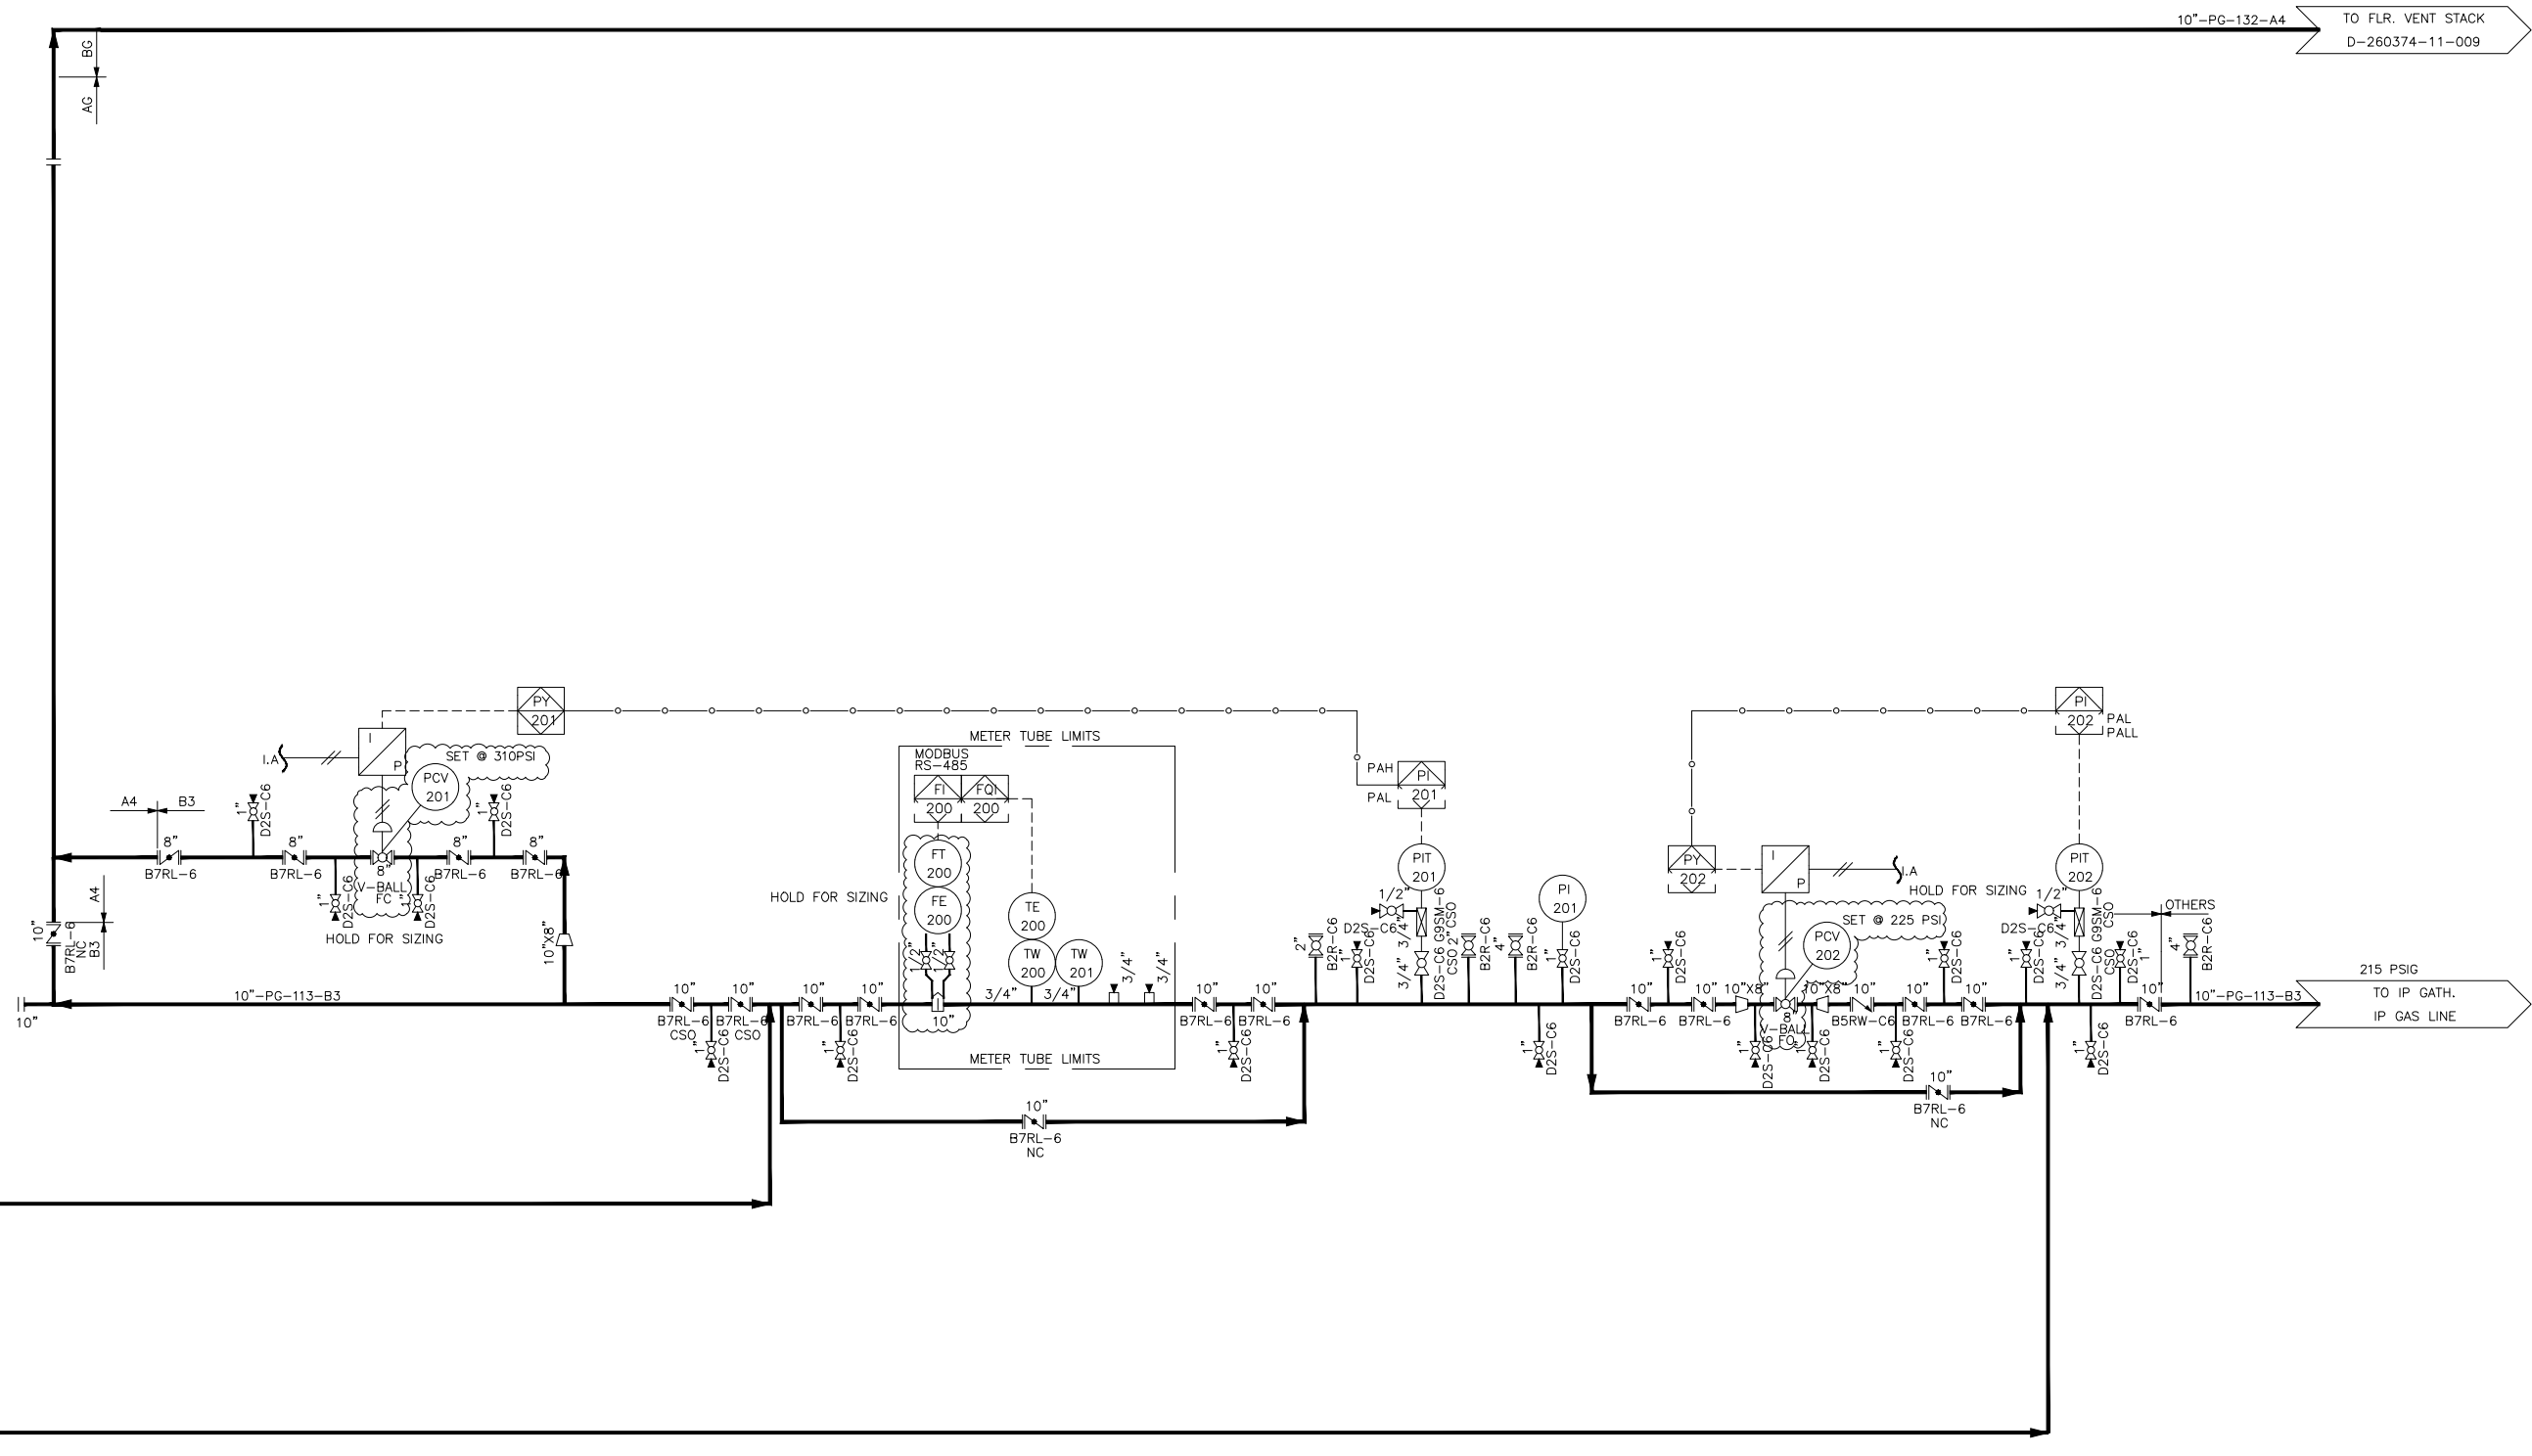

ISSUED
MAY 29, 2026
FOR APPROVAL



NO.	DATE	REVISION	DRW.	DES.	CHK.	APP.	NO.	DATE	REVISION	DRW.	DES.	CHK.	APP.
							A	05/29/26	ISSUED FOR APPROVAL				
							B	06/01/26	ISSUED FOR APPROVAL				

PIPING & INSTRUMENTATION

SCALE: NTS	PLOT SCALE: 1 = 1
AFE:	LOCATION:
DWG. NO: D-260374-11-009	REV. B

DWG NO.

ISSUED
MAY 29, 2026
FOR APPROVAL

V-700
VENT STACK
SIZE: 0'-6" ID

OPERATING PRESSURE: 1 PSIG

FROM SEPARATORS
D-260374-11-009

10"-PG-132-A4

10"x6"

6"

V-700

NOTES:

1. LEVEL GAUGE INSULATION TO BE BLANKET TYPE

3S

ENGINEERING & DESIGN

TSPE FIRM REG. #13809

NM FIRM REG. #454332

OKLA FIRM REG. #3712353615

Ptc: 432-687-5611 Midland, Texas 79705

WWW.3SENGINEERINGDESIGN.COM

REVISION:

NO.	DATE	REVISION	DRW.	DES.	CHK.	APP.	NO.	DATE	REVISION	DRW.	DES.	CHK.	APP.
							A	05/29/26	ISSUED FOR APPROVAL				
							B	06/01/26	ISSUED FOR APPROVAL				

PIPING & INSTRUMENTATION

SCALE: NTS	PLOT SCALE: 1 = 1
AFE:	LOCATION:
DWG. NO: D-260374-11-010	REV. B

DWG NO.

CA-800 AIR COMPRESSOR

TYPE: DUPLEX COMPRESSOR PACKAGE TYPE: 2545A10
MFG/MODEL: IR 2-2545A10
CAPACITY: 35 SCFM @ 125 PSIG (PER PUMP)
RECEIVER TANK: 240 GAL - 250 MAWP
MOTOR: 10 HP - 230-460/3/60 (EACH MOTOR)

F-803
FILTER

TYPE: GENERAL PURPOSE FILTER
MFG/MODEL: IR FA110IG
P) CAPACITY: 65 SCFM

F-804A
PRE-FILTER

TYPE: OIL REMOVAL FILTER
MFG/MODEL: IR FA110IH
CAPACITY: 65 SCFM

DR-804 AIR DRYER


TYPE: DESSICANT AIR DRYER
MFG/MODEL: IR D110IM
CAPACITY: 65 SCFM

F-804B
POST-FILTER

TYPE: DUST FILTER
MFG/MODEL: IR FA110ID
CAPACITY: 65 SCFM

V-805 DRY AIR REVEIVER

SIZE: 30" OD X 7'-0" (240 GAL)
MAWP: 200 PSIG
MAT'L: CARBON STEEL

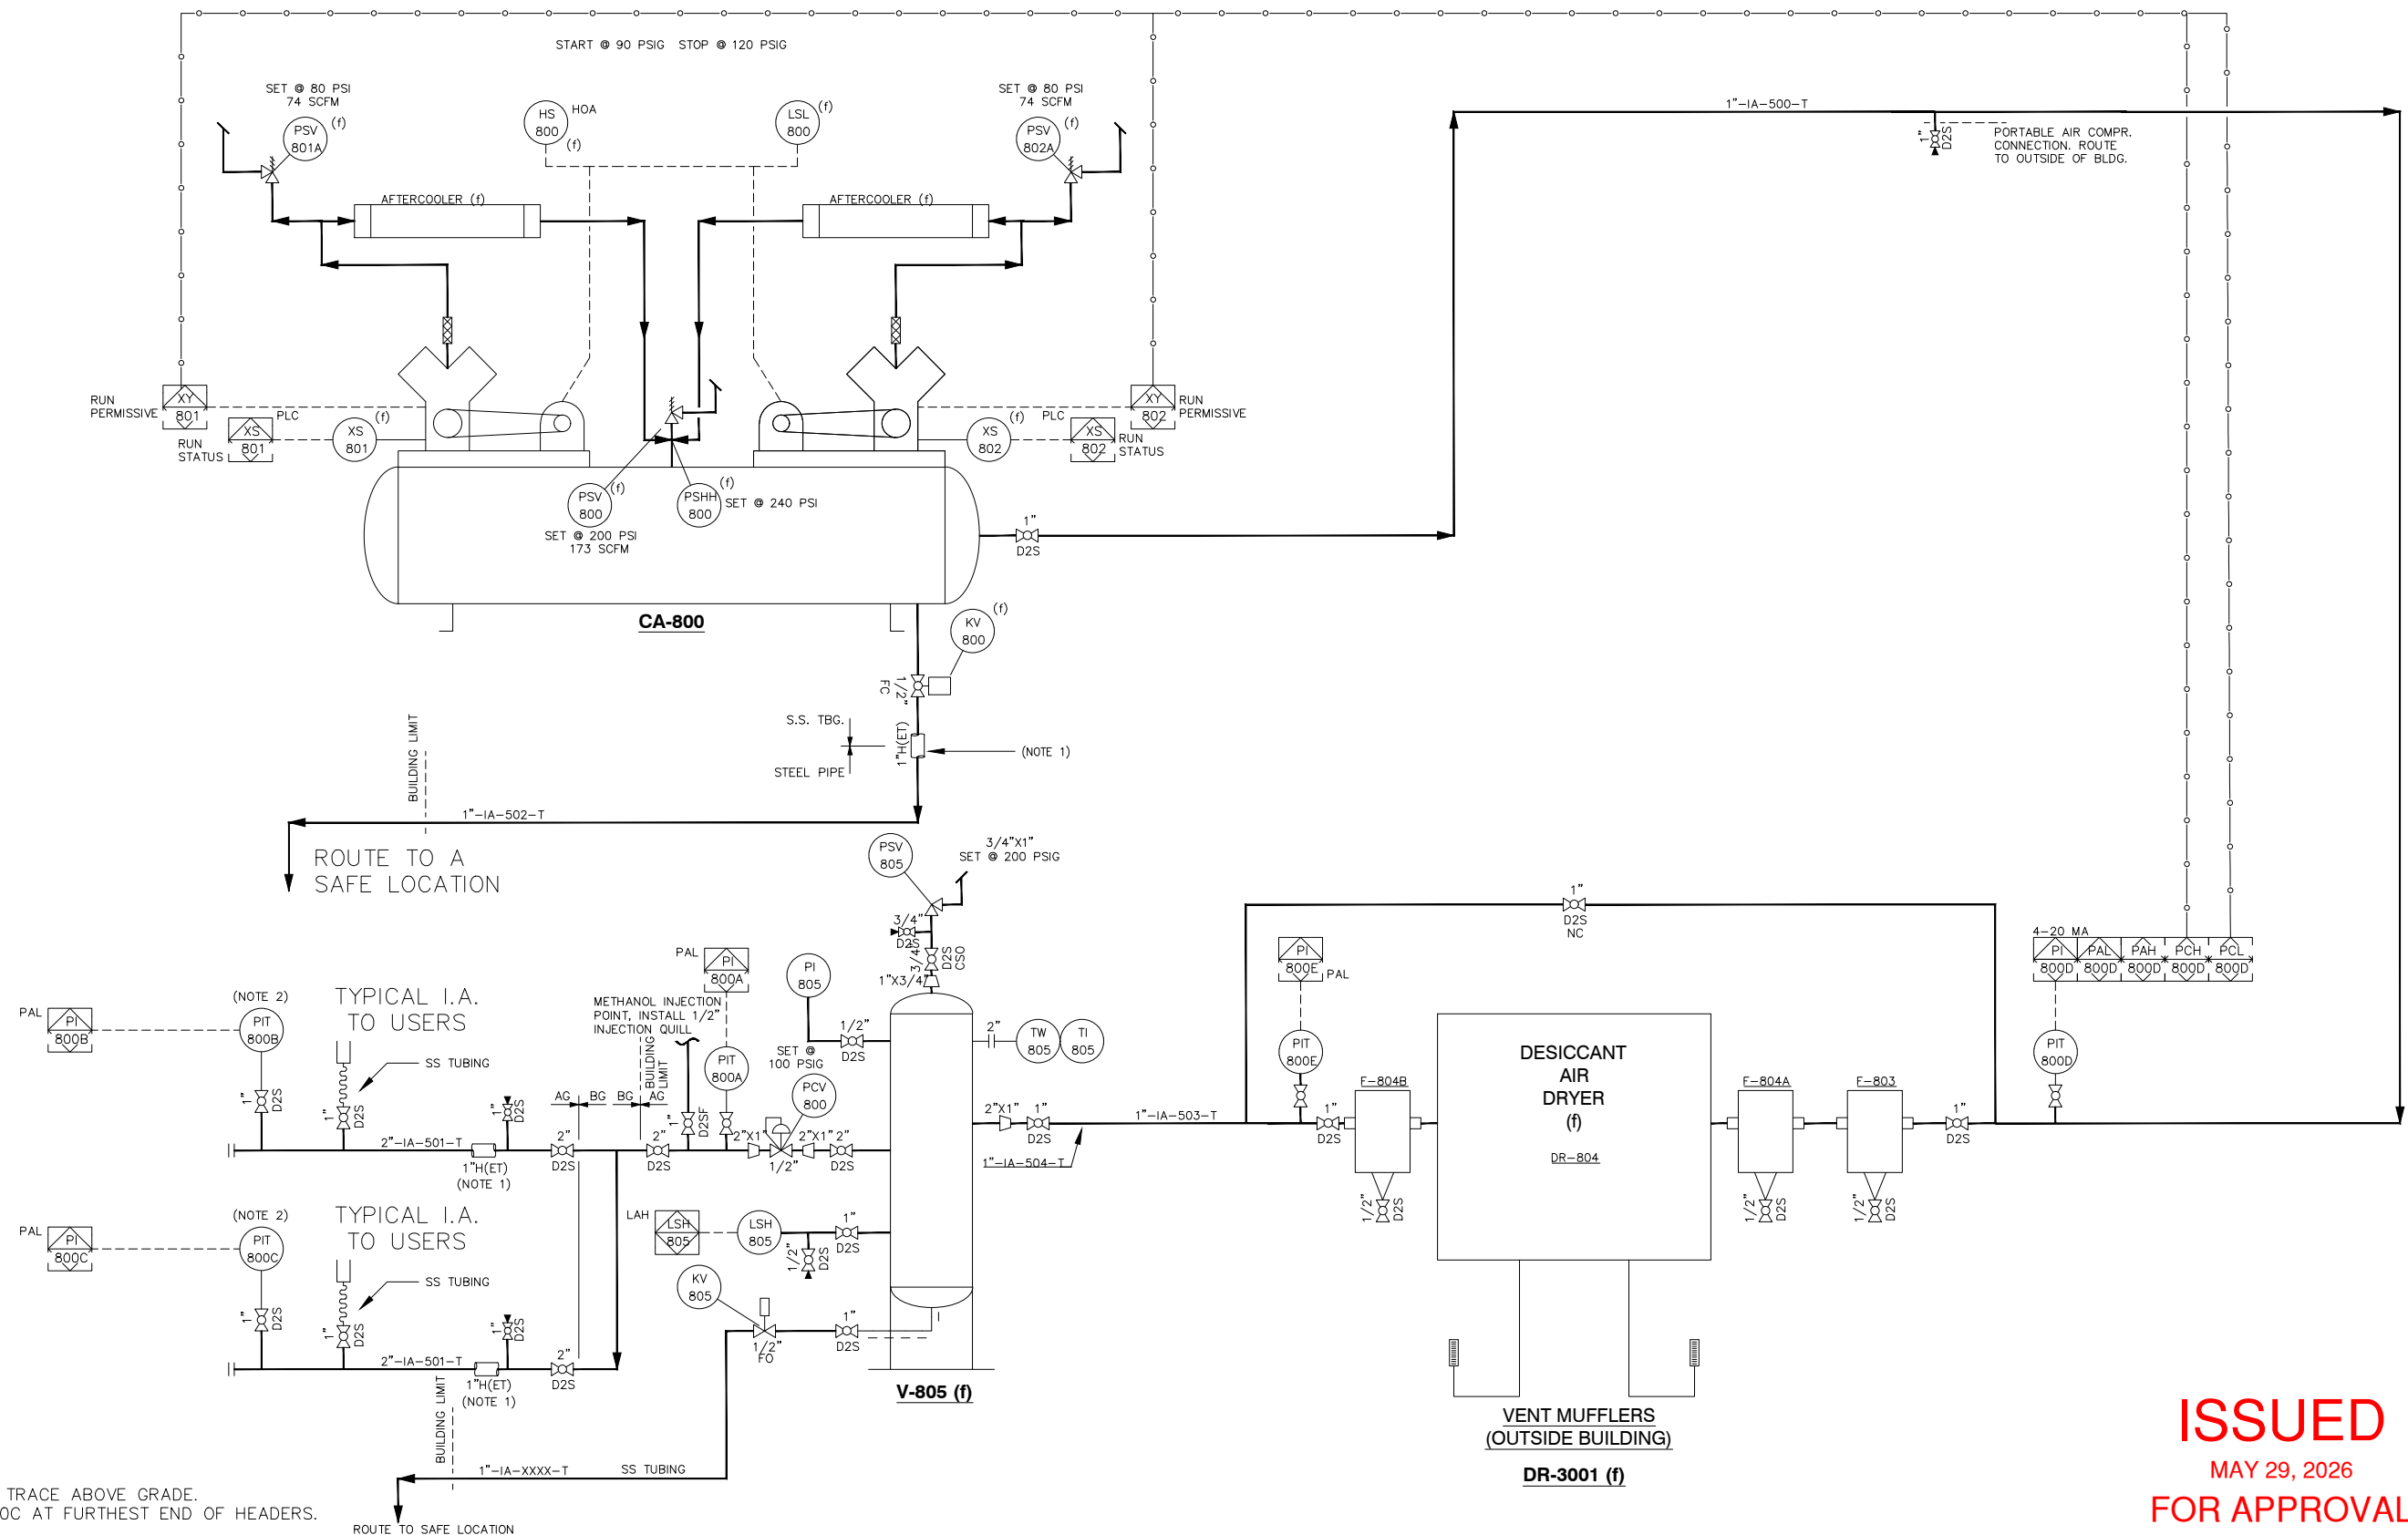

ISSUED
MAY 29, 2026
FOR APPROVAL

3S
ENGINEERING & DESIGN

TBPE FIRM REG. #13809
 NM FIRM REG. #4545320
 OKLA FIRM REG. #3712353615
 Ph: 432-687-5611 Midland, Texas 79705
 WWW.3SENGINEERINGDESIGN.COM

REVISION:

NO.	DATE	REVISION	DRW.	DES.	CHK.	APP.
A	05/29/26	ISSUED FOR APPROVAL				
B	06/01/26	ISSUED FOR APPROVAL				

PIPING & INSTRUMENTATION

SCALE: NTS	PLOT SCALE: 1=1
AFE:	LOCATION:
DWG. NO: D-260374-11-011	REV. B

1

2

3

4

A

B

C

D

INTENTIONALLY BLANK

3S

ENGINEERING & DESIGN

TXPE FIRM REG. #13809

NM FIRM REG. #4545320

OKLA FIRM REG. #2712353615

Ph: 432-687-5611 Midland, Texas 79705

WWW.3SENGINEERINGDESIGN.COM

REVISION:

NO.	DATE	REVISION	DRW.	DES.	CHK.	APP.	NO.	DATE	REVISION	DRW.	DES.	CHK.	APP.
							A	05/29/26	ISSUED FOR APPROVAL				
							B	06/01/26	ISSUED FOR APPROVAL				

PIPING & INSTRUMENTATION

SCALE: NTS	PLOT SCALE: 1 = 1
AFE:	LOCATION:
DWG. NO: D-260374-11-004	REV. B

DWG NO.