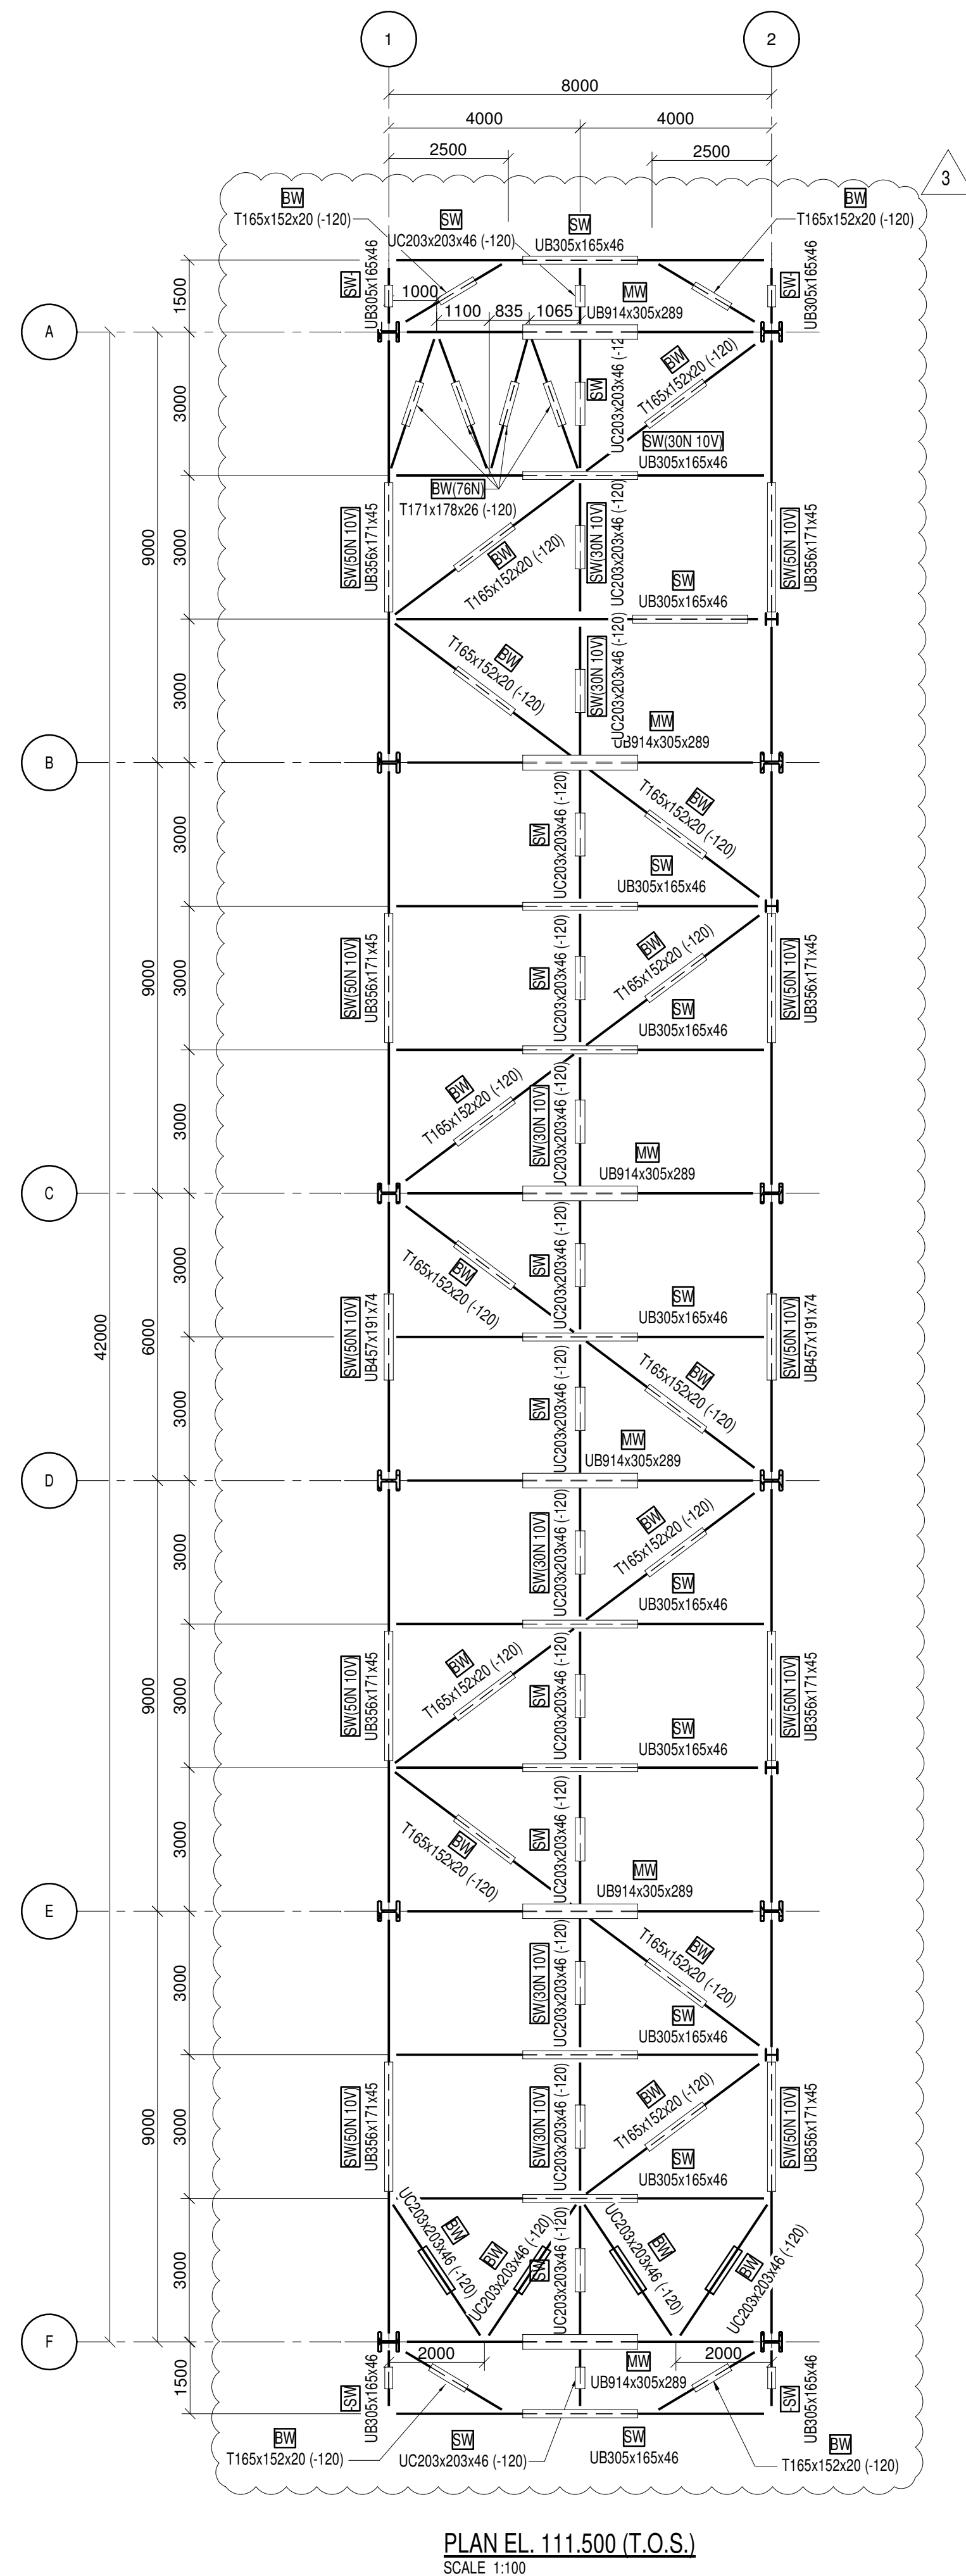



[illegible]

1. FOR GENERAL NOTES, REFERENCES DRAWINGS AND KEYPLAN SEE SHEET 001.

REFERENCE DRAWINGS / DOCUMENTS

DRAWING NUMBER	DRAWING TITLE

KEY PLAN

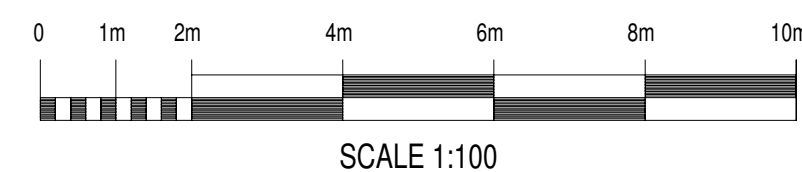[illegible]

CONSULTANT/CONTRACTOR/VENDOR	 TECNICAS REUNIDAS
DRAWING No.	AD-3010-C-330030-SHT-004

PROJECT/PMR TITLE LOWER ZAKUM LONG TERM DEVELOPMENT
PLAN PHASE-1 (LZ LTDP-1) - EPC WORKS PACKAGE 2



أدنوك البحرية
ADNOC Offshore

DRAWING TITLE UTILITIES (NITROGEN SYSTEM, INSTRUMENT/PLANT AIR, POTABLE WATER)-UNIT 3010
AL OMAIRAH ISLAND
3010PAR002 STEEL STRUCTURE
PLAN EL. 111.500 & 112.800 (T.O.S.)

BUDGET REF. 14001-10222-2		DRAWING No. AD-3010-C-330030-SHT-004	SHT.No.	REV.
PROJ/PMR No. 10222-2	SCALE AS SHOWN		004	3

SHT. SIZE: A1